



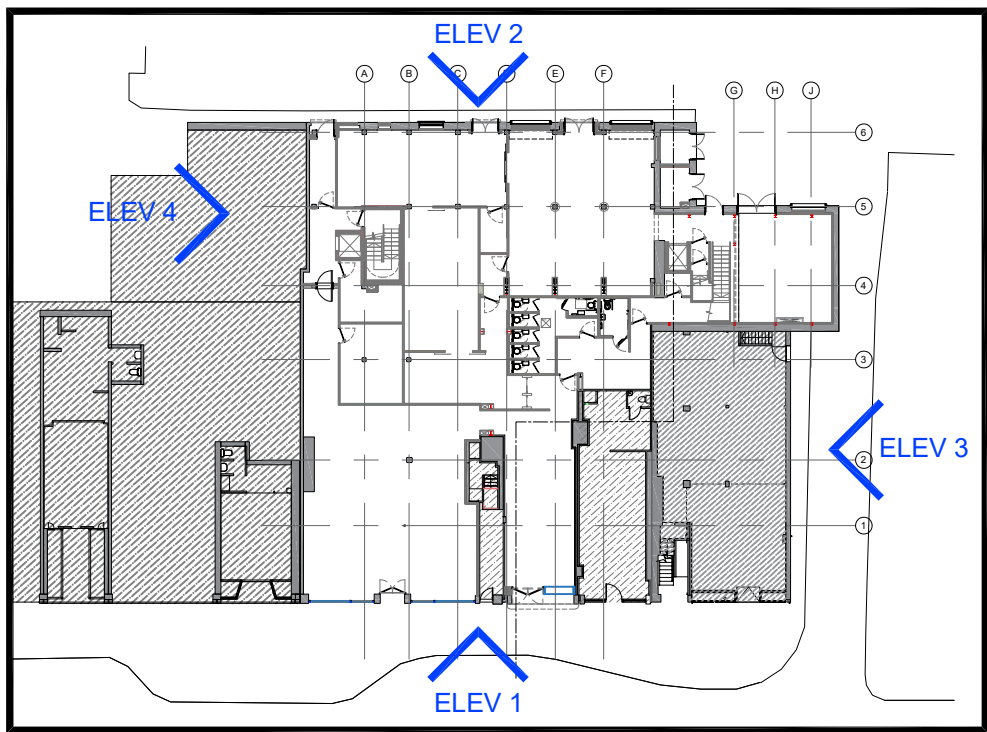


1
30.10

GFL_KEYPLAN
SCALE: NTS

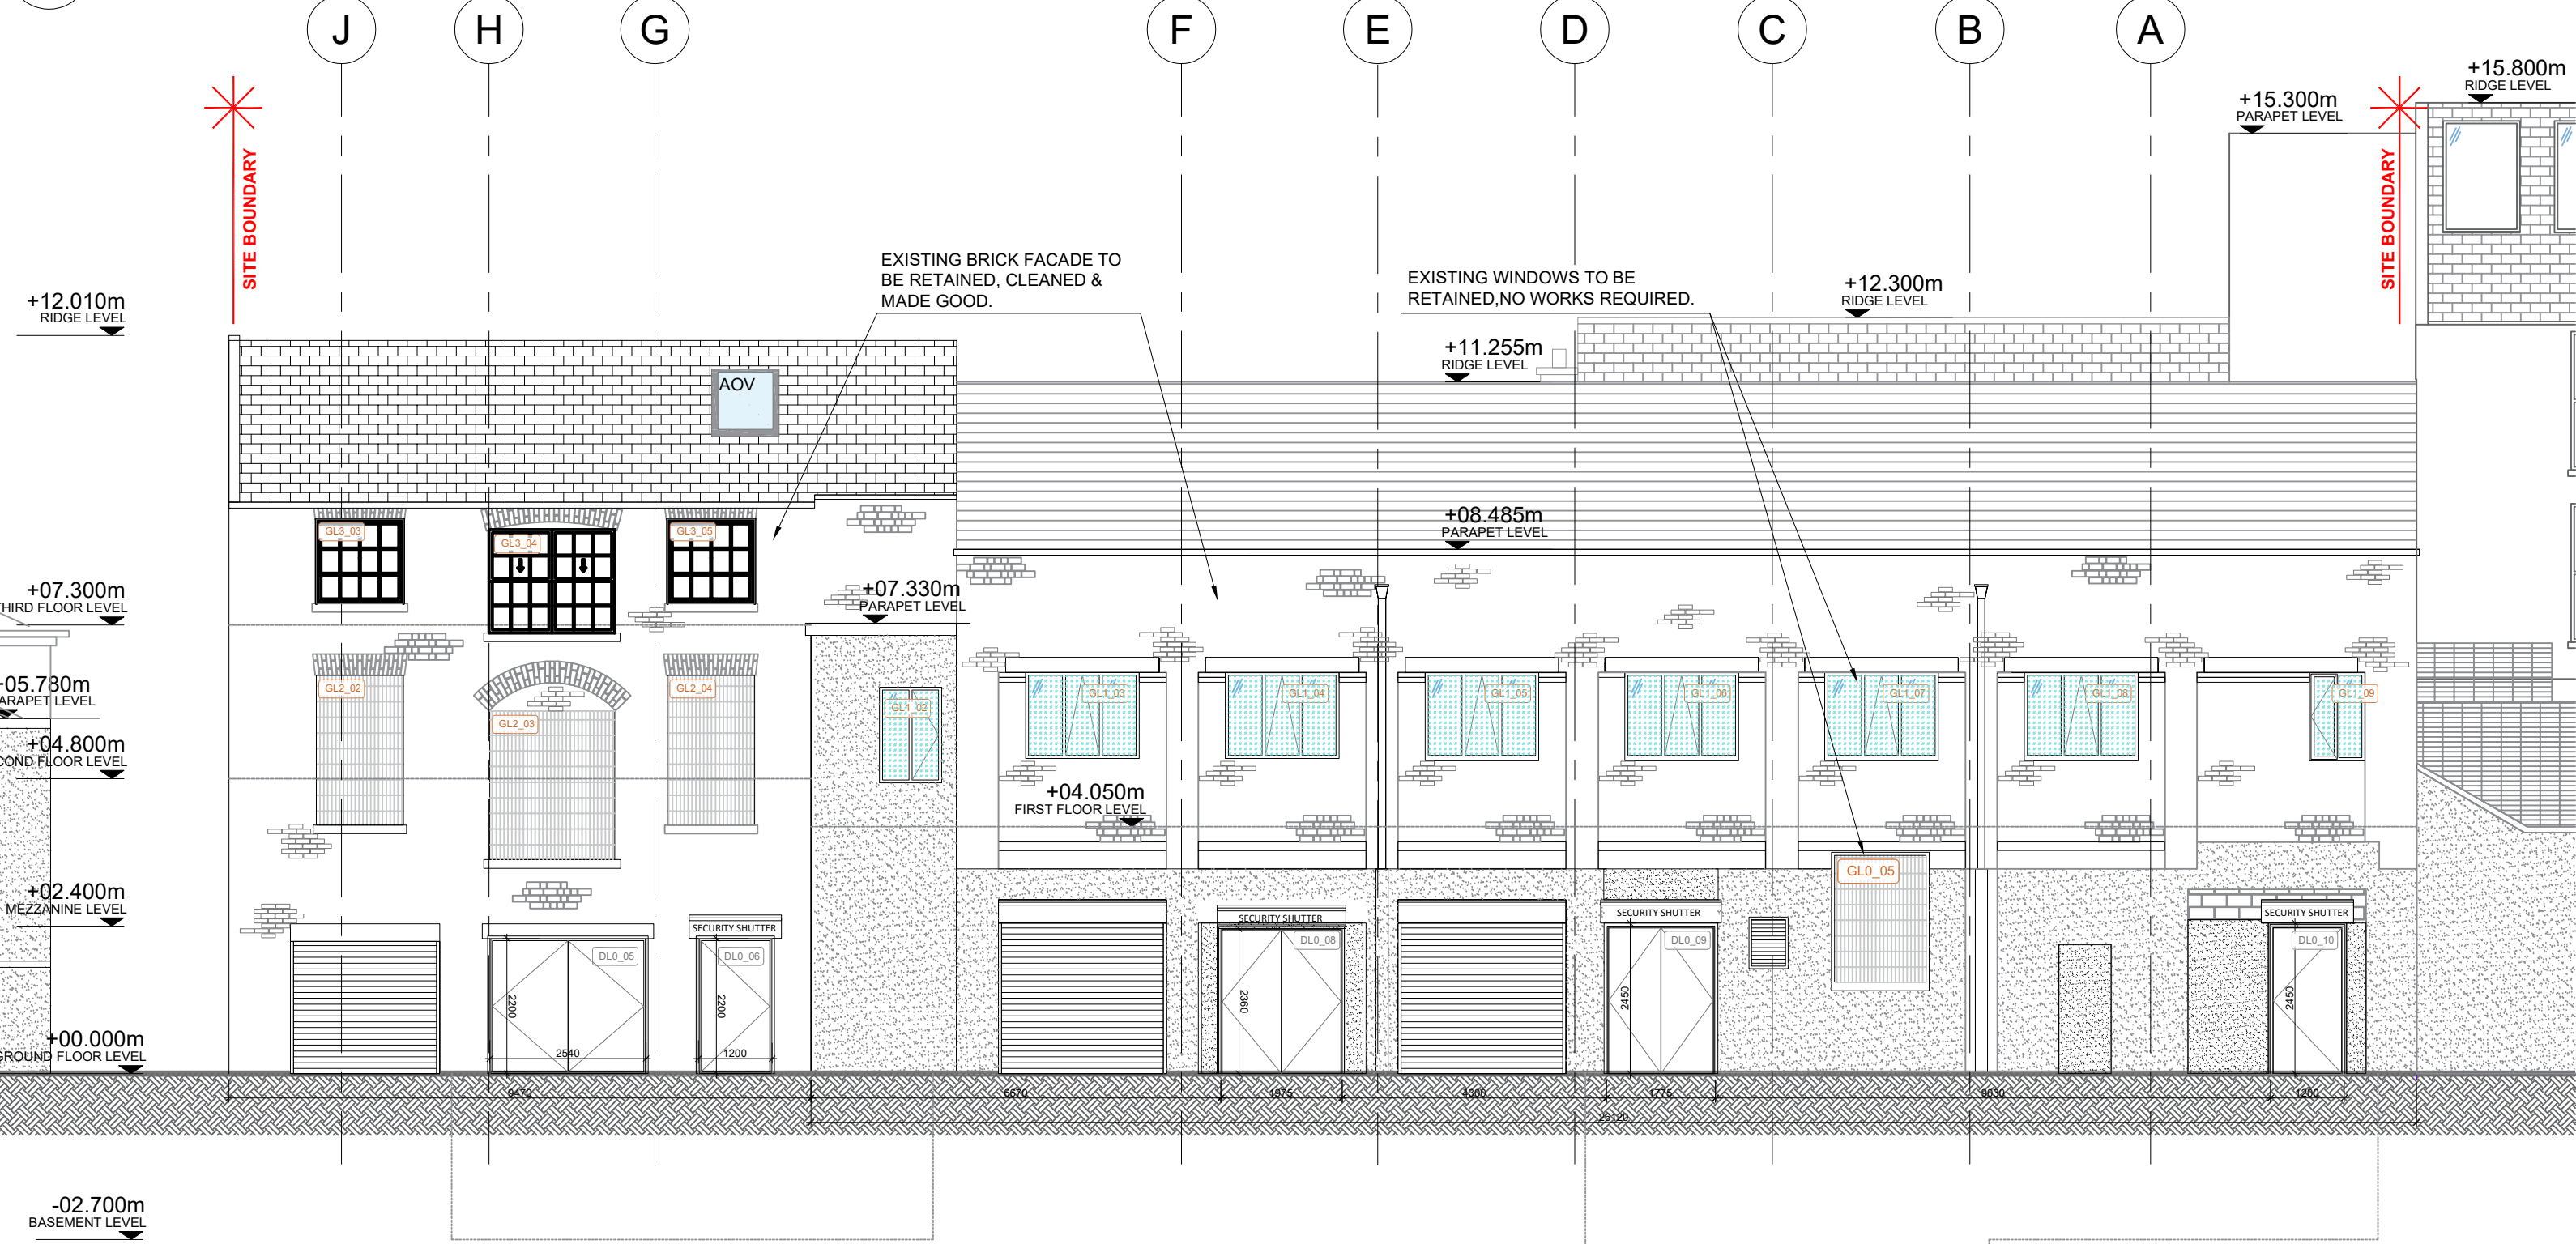


2
30.10

SOUTH ELEVATION_MARLBOROUGH PLACE
SCALE: 1:100

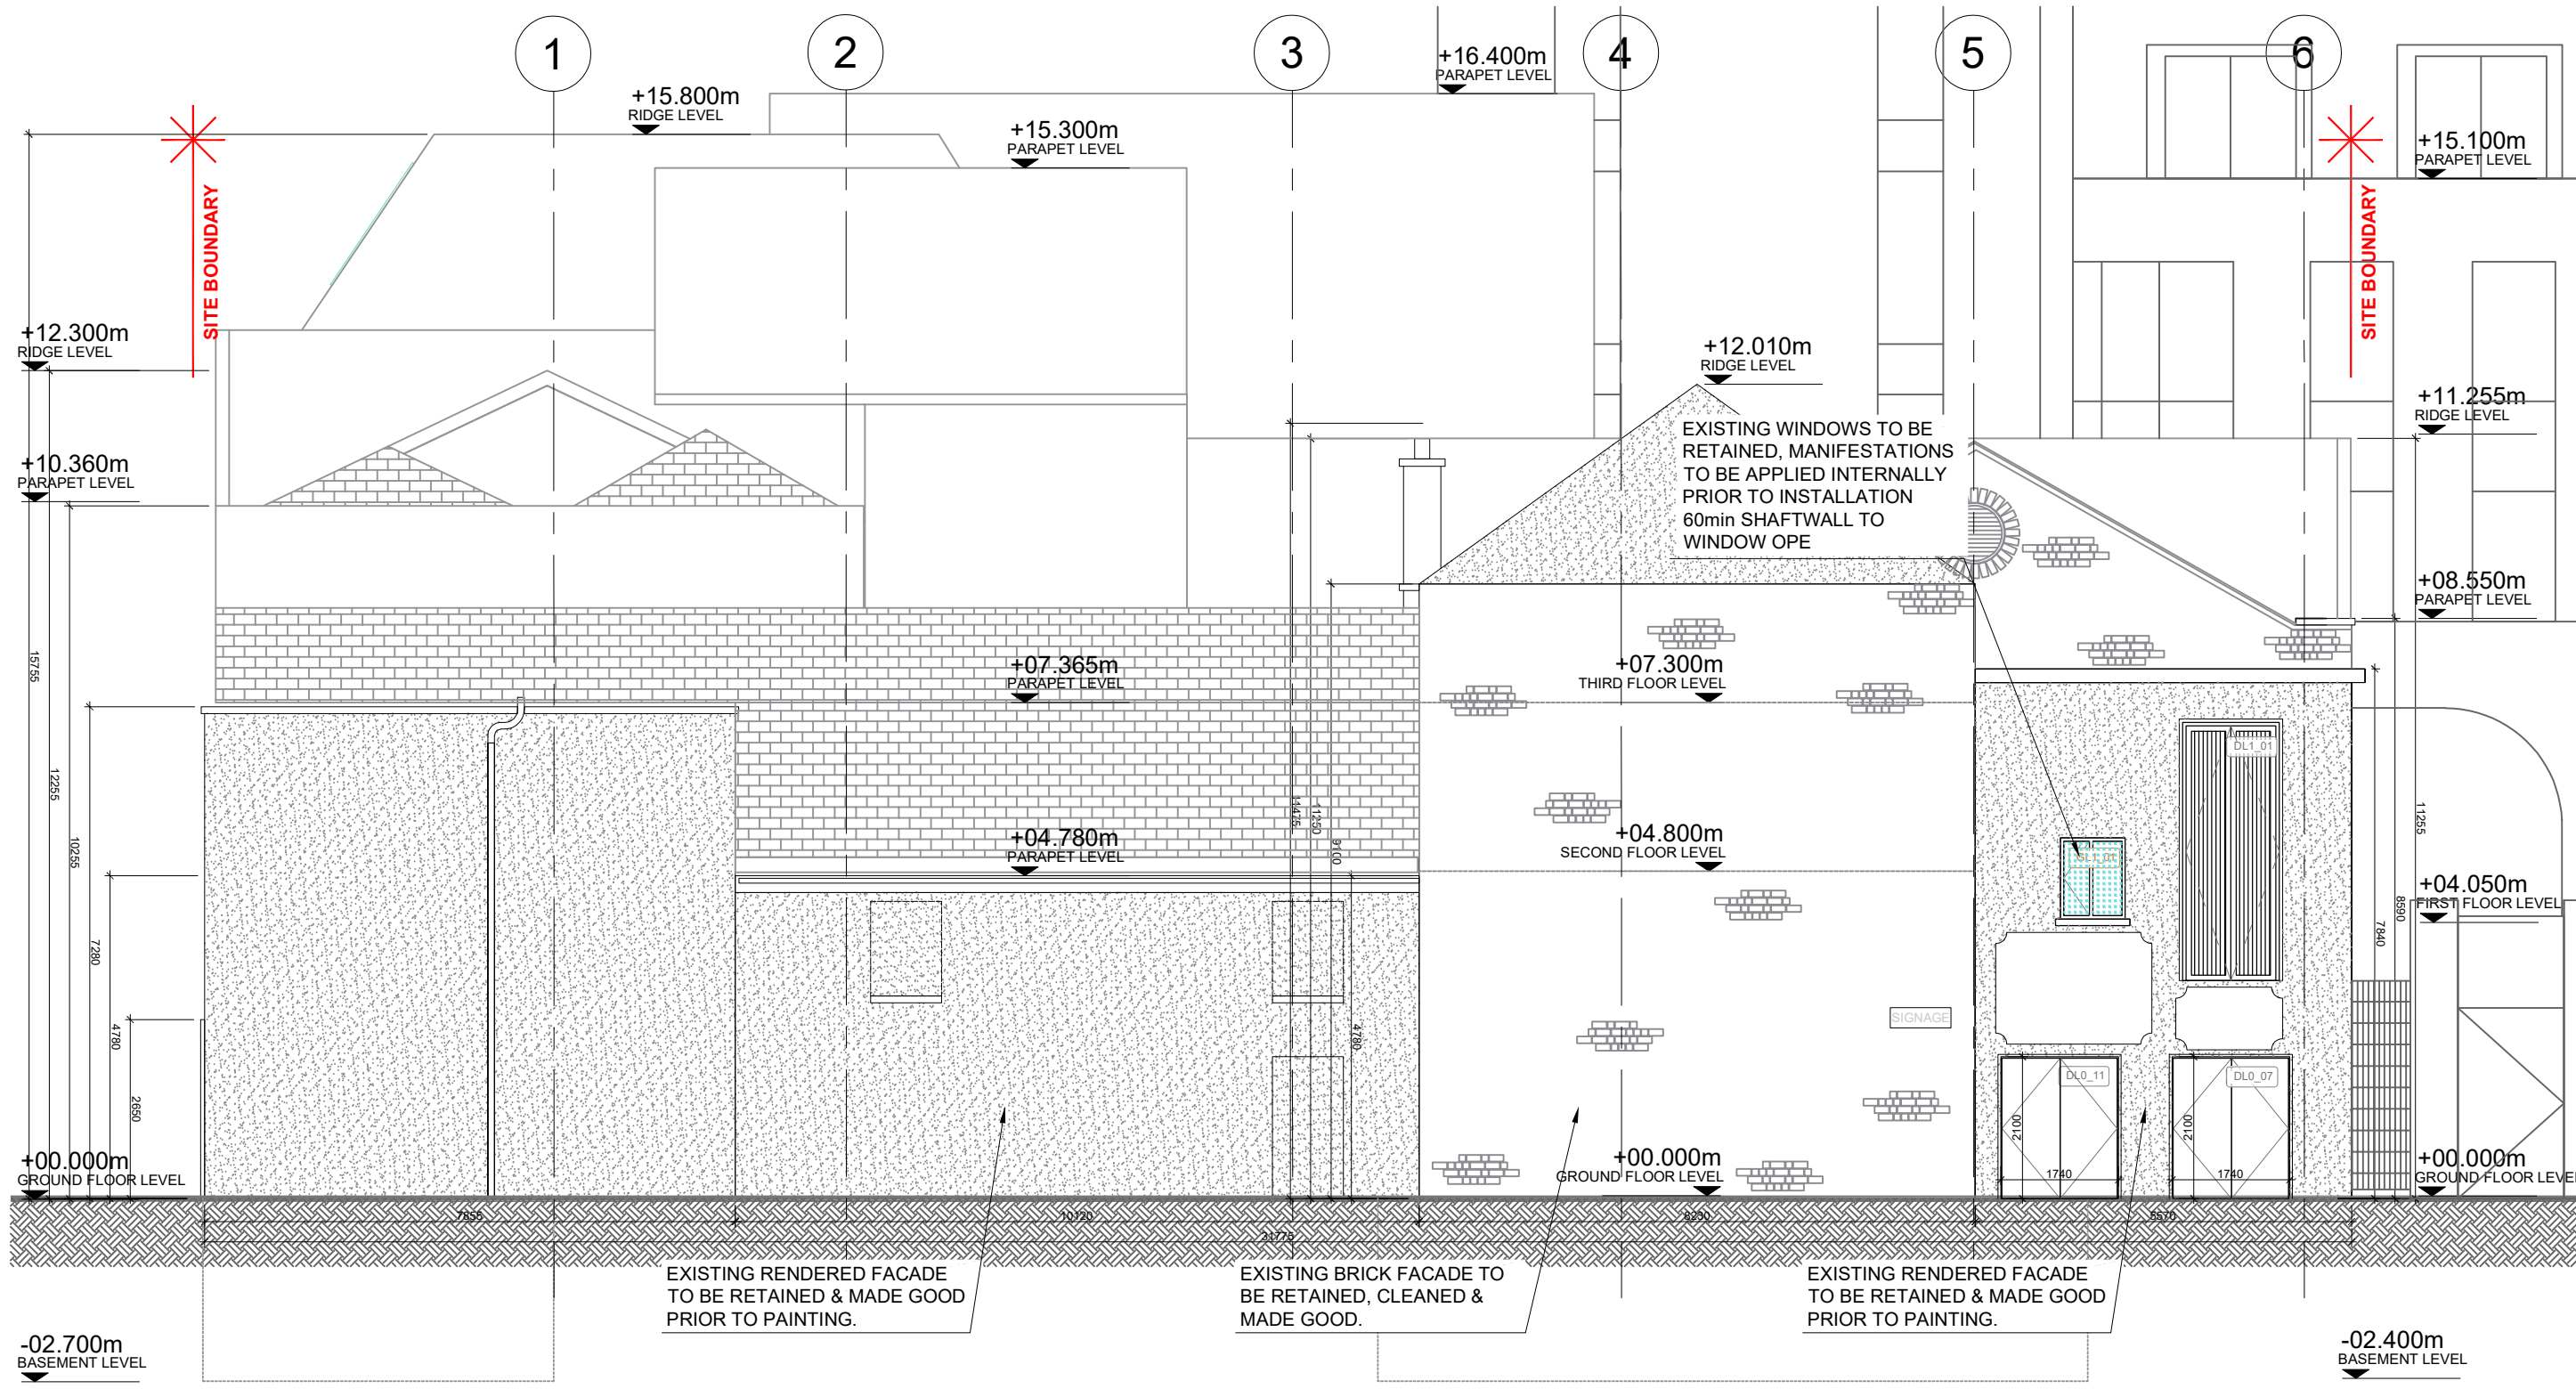


3
30.10

WEST ELEVATION_TALBOT LANE
SCALE: 1:100

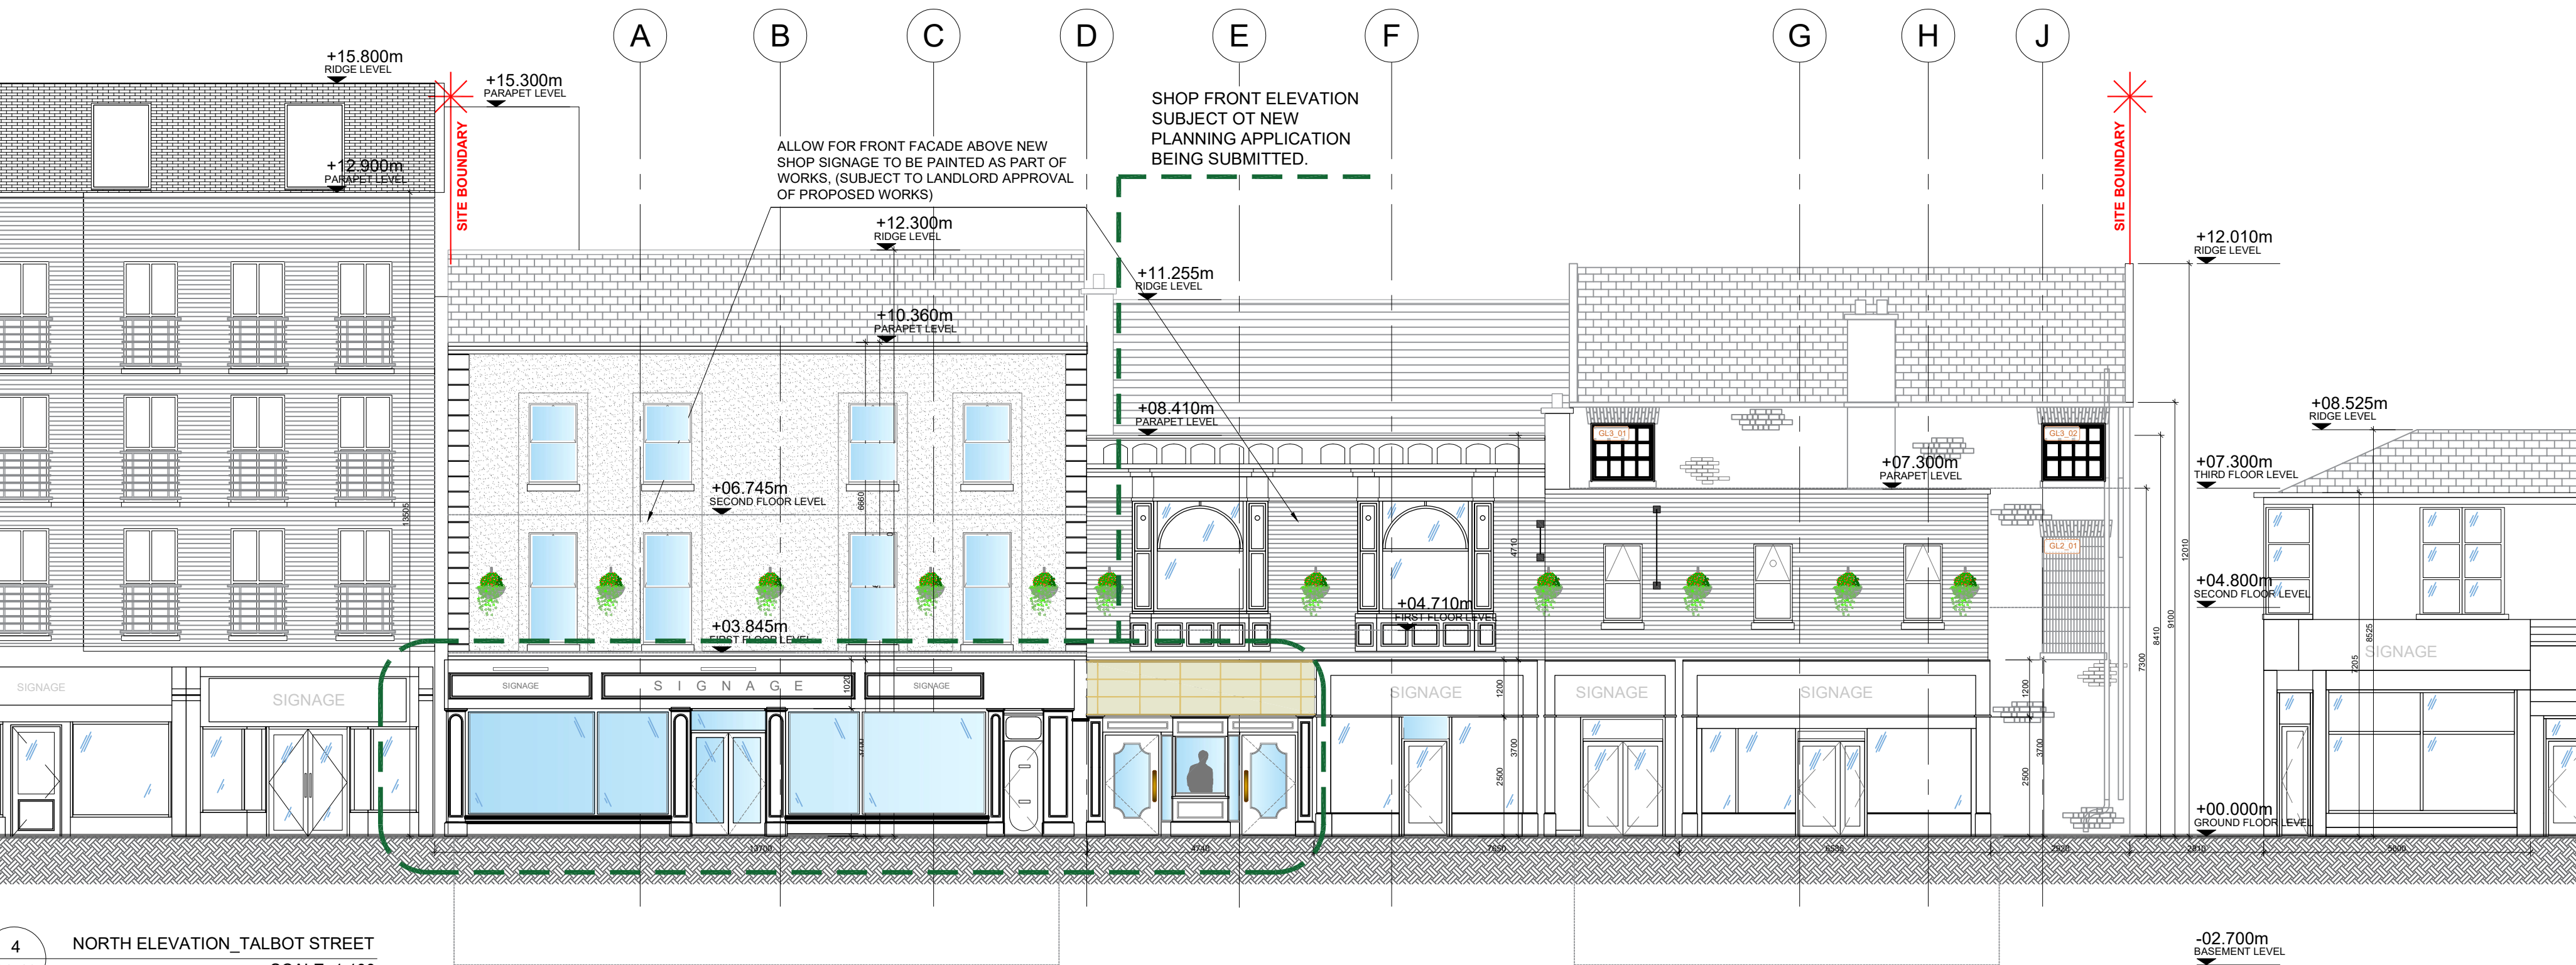

4
30.10

NORTH ELEVATION_TALBOT STREET
SCALE: 1:100

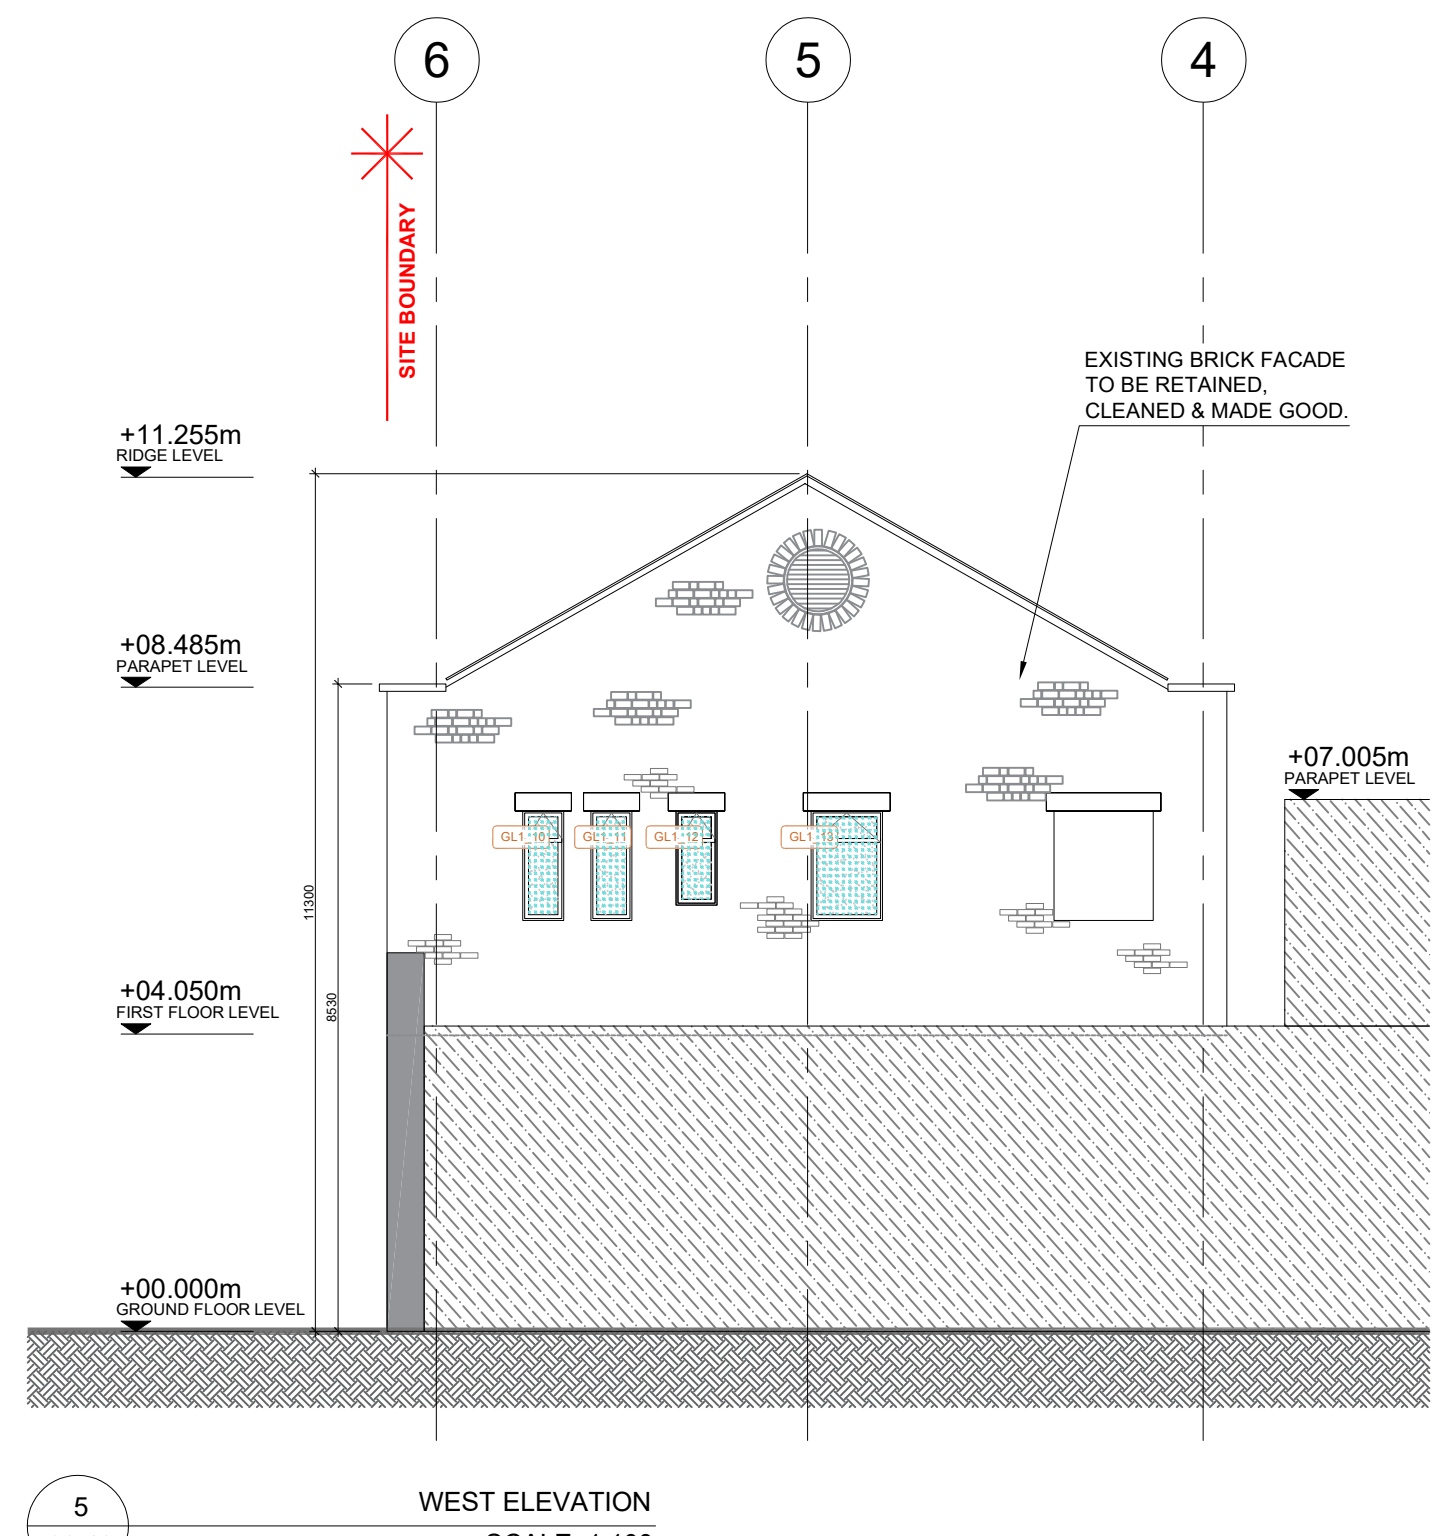

5
30.10

WEST ELEVATION
SCALE: 1:100

Legend

- AREA OUTSIDE SCOPE OF WORKS
- INTERIOR ROOM No.
- INTERIOR DOOR No.
- FIXED JOINERY No.
- INTERNAL GLAZED SCREEN No.
- EXTERNAL GLAZING No.
- EXTERNAL DOOR No.
- SET PIECE No.

Notes:

To be read in conjunction with all relevant drawings & schedules, refer to drawing register for breakdown of drawings.

Drawing to be printed in colour.

A1

Do not scale drawing, work to figured dimensions. All dimensions to be checked on site. Any errors or discrepancies to be reported to MILLIMETRE DESIGN. This drawing may not be edited or modified without permission. This drawing is to be read in colour and in conjunction with all relevant consultant and specialist drawings, schedules and documentation. Only build from drawings issued as Construction.

#	13.03.26	SMC	FIRST ISSUE
REV	DATE	APP BY	DESCRIPTION
4 Ongar Square, Ongar Village, Dublin 15. D15 H34C			
+353 1 826 3971 info@millimetre design.com			
www.millimetre design.com			
This drawing is the property of Millimetre Design Ltd & must not be reproduced without prior consent.			
CLIENT	Carrolls Irish Gifts		
PROJECT ADDRESS	Immersive Experience		
DWG TITLE	Talbot Street, North City, Dublin 1, D01 X652		
EDITION	EXTERIOR ELEVATIONS PROPOSED ELEVATIONS		
DWG NO	TENDER		
REV	PROJECT NO	SCALE	
#	CIX	1:100	
DATE	FEB 2026	DRN	SMC