

Legend

LX_XX

INTERIOR ROOM No.

DRX_XX

INTERIOR DOOR No.

JTX_XX

FIXED JOINERY No.

GSX_XX

INTERNAL GLAZED SCREEN No.

GLX_XX

EXTERNAL GLAZING No.

DLX_XX

EXTERNAL DOOR No.

SPX_XX

SET PIECE No.

60min FIRE RESISTANCE BLOCKWORK

60min FIRE RESISTANCE PARTITION

30min FIRE RESISTANCE PARTITION

NON FIRE RESISTANCE PARTITION

INSULATED PLASTERBOARD


60min / ACOUSTIC INFILL PLASTERBOARD SECTIONS

60min SHAFTWALL PLASTERBOARD SECTIONS

Notes:

To be read in conjunction with all relevant drawings & schedules, refer to drawing register for breakdown of drawings.

Drawing to be printed in colour.

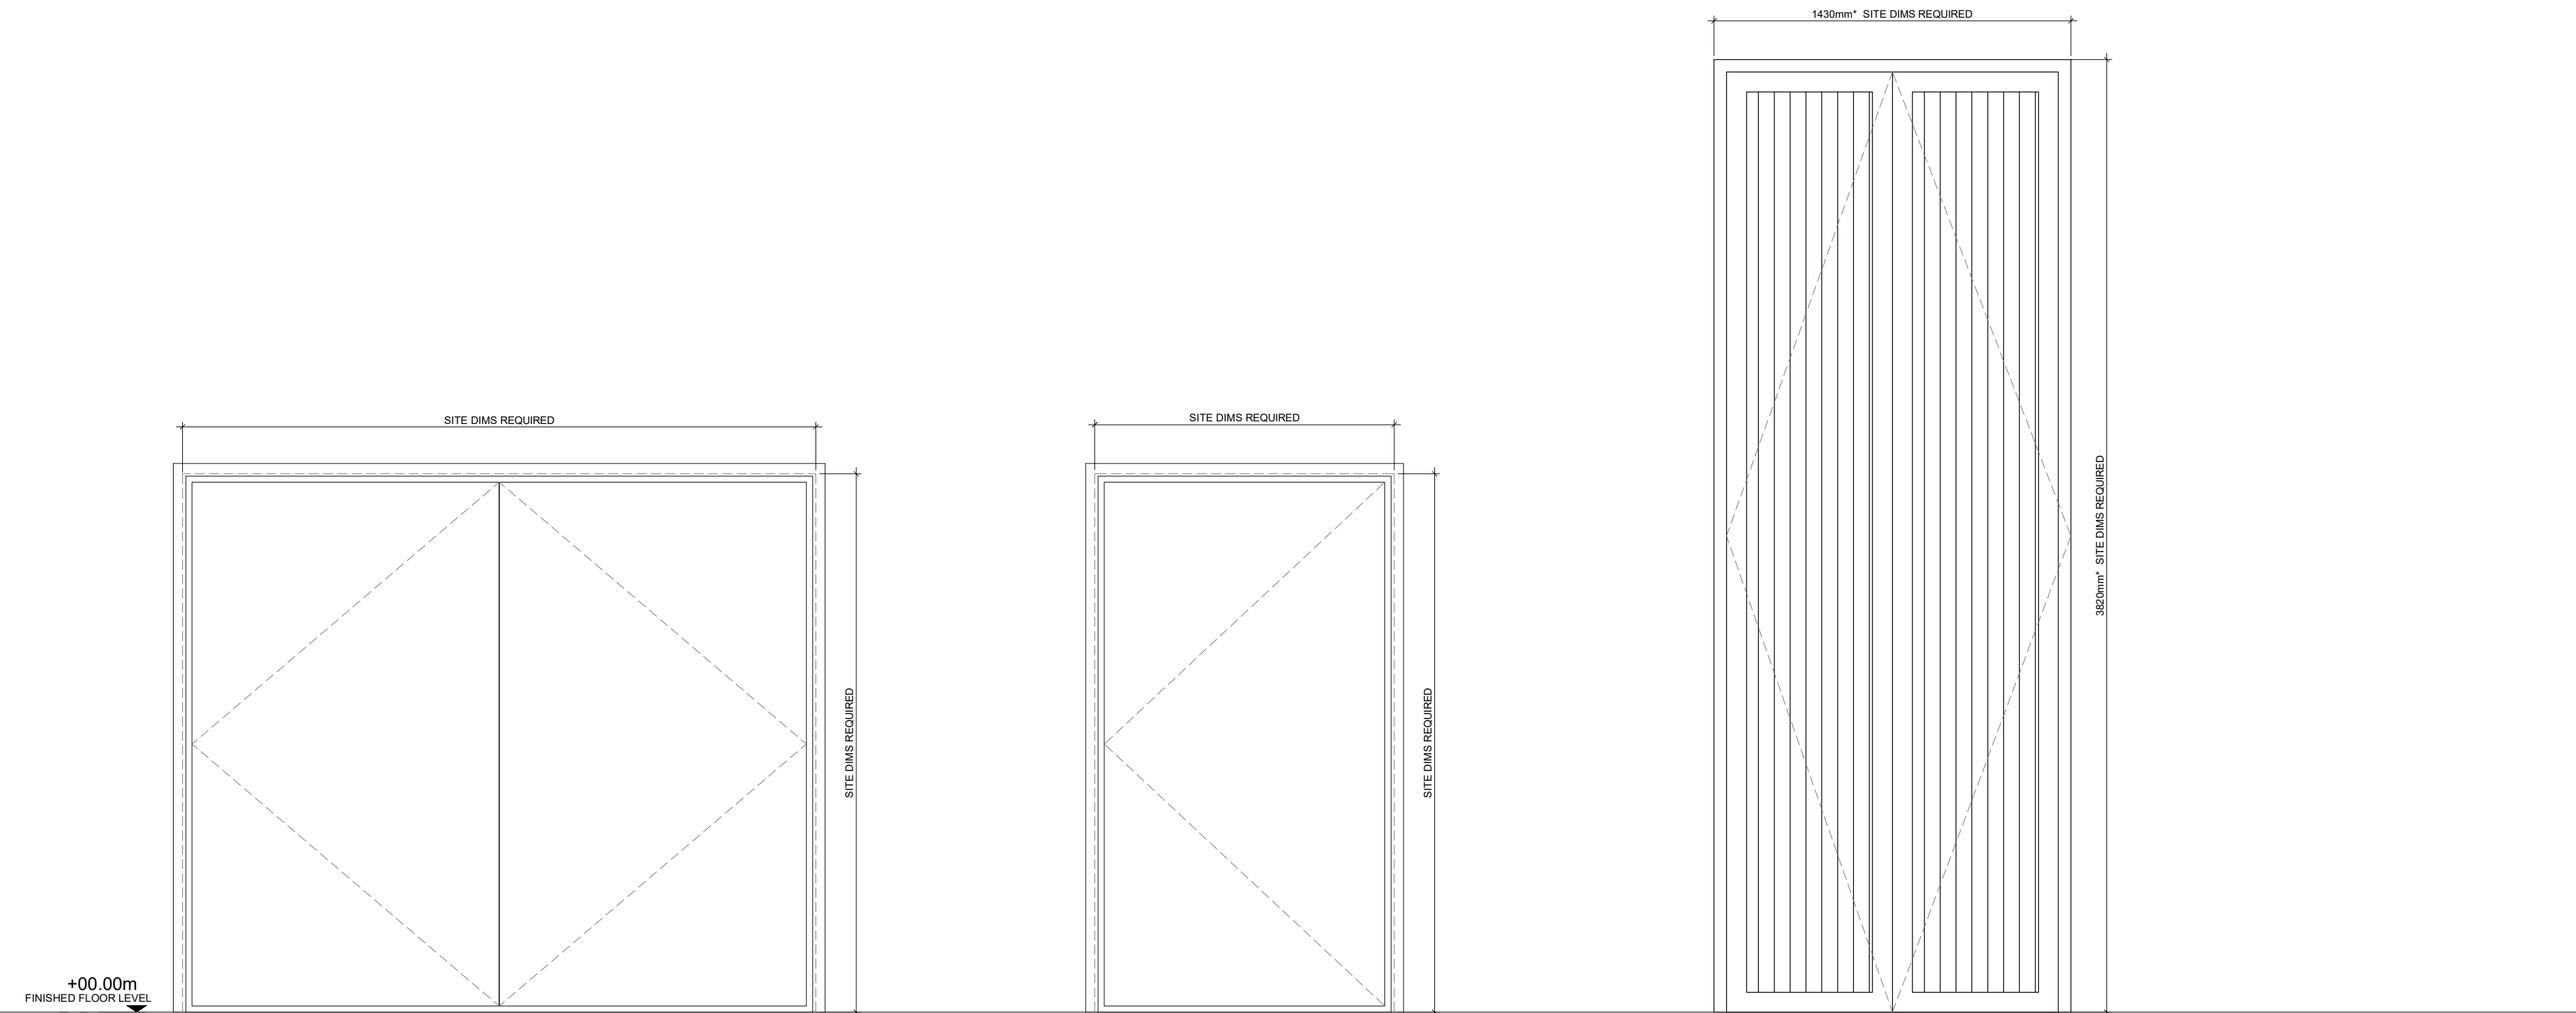

DL0_06	STRUCTURAL OPE:	2540mm (W) x 220mm (H)
DL0_07	STRUCTURAL OPE:	1740mm (W) x 2100mm (H)
DL0_08	STRUCTURAL OPE:	1975mm (W) x 2360mm (H)
DL0_09	STRUCTURAL OPE:	1775mm (W) x 2450mm (H)
DL0_11	STRUCTURAL OPE:	1740mm (W) x 2100mm (H)

DL0_06	STRUCTURAL OPE:	1200mm (W) x 2200mm (H)
DL0_10	STRUCTURAL OPE:	1275mm (W) x 2450mm (H)

DL1_01	STRUCTURAL OPE:	1430mm (W) x 3820mm (H)
--------	-----------------	-------------------------

1	EXTERNAL DOOR_ TYPE 1
50.00	SCALE: 1:20
DOOR REFERENCE MARK:	DL0_06 DL0_07 DL0_08 DL0_09 DL0_11
PROPOSED / EXISTING:	PROPOSED ALUMINIUM DOUBLE DOOR AND FRAME
FRAME MATERIAL:	NEW ALUMINIUM FRAME
FRAME FINISH:	SELECTED EXTERNAL RAL PPC FINISH
COLOUR:	NEW SELECTED COLOUR_RAL TBC
OPENING TYPE:	OUTWARD OPENING
GLASS:	N/A
HARDWARE:	MANUF: STANDARD TO BE READ IN CONJUNCTION WITH FIRE CERT REQUIREMENTS.
CURTAINS / BLINDS	N/A

2	EXTERNAL DOOR_ TYPE 2
50.00	SCALE: 1:20
DOOR REFERENCE MARK:	DL0_06 DL0_10
PROPOSED / EXISTING:	PROPOSED ALUMINIUM SINGLE DOOR AND FRAME
FRAME MATERIAL:	NEW ALUMINIUM FRAME
FRAME FINISH:	SELECTED EXTERNAL RAL PPC FINISH
COLOUR:	NEW SELECTED COLOUR_RAL TBC
OPENING TYPE:	OUTWARD OPENING
GLASS:	N/A
HARDWARE:	MANUF: STANDARD TO BE READ IN CONJUNCTION WITH FIRE CERT REQUIREMENTS.
CURTAINS / BLINDS	N/A

3	EXTERNAL DOOR_ TYPE 3
50.00	SCALE: 1:20
DOOR REFERENCE MARK:	DL1_01
PROPOSED / EXISTING:	NEW HARDWOOD FRAME & 57mm DOUBLE SHEETED DOUBLE DOOR TO REPLICATE EXISTING DOOR BEING REMOVED.
FRAME MATERIAL:	NEW HARDWOOD FRAME
FRAME FINISH:	SELECTED EXTERNAL RAL FINISH
COLOUR:	NEW SELECTED COLOUR_RAL TBC
OPENING TYPE:	NON OPERATIONAL FIXED DOORS
GLASS:	N/A
HARDWARE:	N/A
CURTAINS / BLINDS	N/A

#	13.03.26	SMC	FIRST ISSUE
REV	DATE	APP BY	DESCRIPTION
MILLIMETRE DESIGN 4 Ongar Square, Ongar Village, Dublin 15. D15 H34C +353 1 826 3971 info@millimetredesign.com www.millimetredesign.com			
This drawing is the property of Millimetre Design Ltd & must not be reproduced without prior consent.			
CLIENT	Carrolls Irish Gifts Immersive Experience		
PROJECT ADDRESS	Talbot Street, North City, Dublin 1, D01 X652		
DWG TITLE	EXTERNAL DETAILS DOOR ELEVATIONS		
EDITION	TENDER		
DWG NO	CIX-TD-50.00		
REV	PROJECT NO	SCALE	
#	CIX	1:20	
DATE	FEB 2026	DRN	SMC APP