
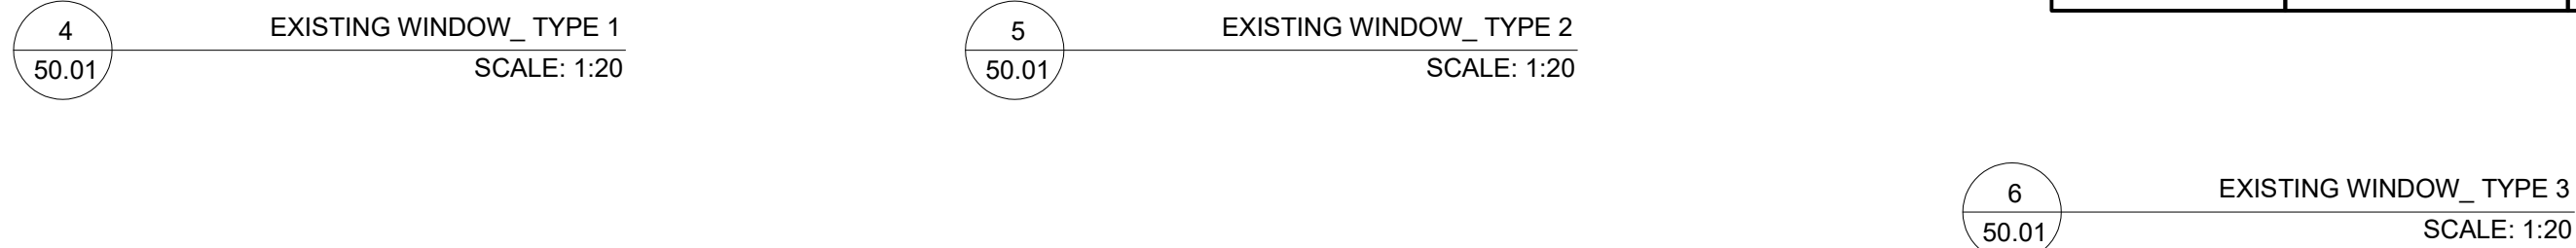


- HARDWOOD SLIDING SASH WINDOW, FINAL RAL COLOUR TBC. FULL PANE OF GLASS TO EACH SASH WITH SPACER BARS BETWEEN GLAZING WITH TIMBER GLAZING BARS FIXED TO GLAZING.
- TRADITIONAL WEIGHTS & CORDS NOT REQUIRED, STYLE OF EXISTING WINDOWS BEING REMOVED TO BE REPLICATED.
- CLEAR DOUBLE GLAZING WITH 24mm TOUGHENED GLASS AS REQUIRED FOR FIXED SECTIONS OF WINDOWS.
- ALL EXISTING STRUCTURAL OPES TO BE MEASURED PRIOR TO SHOP DRAWINGS BEING ISSUED FOR APPROVAL.
- ALLOW FOR NEW WINDOWS BOARDS TO BE INSTALLED AS PART OF PHASE 3 FITOUT WORKS.

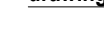

- EXISTING FRAMES TO BE RETAINED IN SITU & INSPECTED TO DETERMINE EXTENT OF REPAIRATION / REPLACEMENT IF ANY REQUIRED.
- ALLOW FOR REMEDIAL WORKS TO BE CARRIED OUT TO 4no. EXISTING WINDOWS BEING RETAINED WITHIN GALLERY BUILDING, MAKE GOOD ANY BROKEN PANES & DEEP CLEAN IN PREPARATION OF INSTALLATION OF MANIFESTATIONS.
- EXISTING WINDOWS WITHIN GALLERY BUILDING TO BE PAINTED EXTERNALLY.
- ALL WINDOWS TO HAVE FIXED / NON OPENABLE SECTIONS.
- ALLOW FOR INSPECTION OF WINDOW GL0_05 TO DETERMINE EXTENT OF WORKS REQUIRED, REMEDIAL WORKS AS REQUIRED INLINE WITH WORKS LISTED ABOVE.
- REMEDIAL WORKS TO GL2_01 & GL2_02 TO BE COORDINATED WITH M&E VENTING REQUIREMENTS FOR THE WC's, POSSIBLE VENT INSTALLATION WITHIN WINDOW FRAMES, EXACT POSITIONS TBC.
- INCLUDE FOR MANIFESTATIONS TO BE INSTALLED TO ALL EXISTING WINDOWS IN EXISTING GALLERY BUILDING, SPEC TBC. REFER TO DWG 30.10 FOR EXACT LOCATIONS.

Legend	
	AREA OUTSIDE SCOPE OF WORKS
	INTERIOR ROOM No.
	INTERIOR DOOR No.
	FIXED JOINERY No.
	INTERNAL GLAZED SCREEN No.
	EXTERNAL GLAZING No.
	EXTERNAL DOOR No.
	SET PIECE No.
	60min FIRE RESISTANCE BLOCKWORK
	60min FIRE RESISTANCE PARTITION
	30min FIRE RESISTANCE PARTITION
	NON FIRE RESISTANCE PARTITION
	INSULATED PLASTERBOARD
	60min ACUSTIC INFILL PLASTERBOARD SECTIONS
	60min SHAFTHALL PLASTERBOARD SECTIONS

Notes:

To be read in conjunction with all relevant drawings & schedules, refer to drawing register for breakdown of drawings.

Drawing to be printed in colour.

[illegible]