



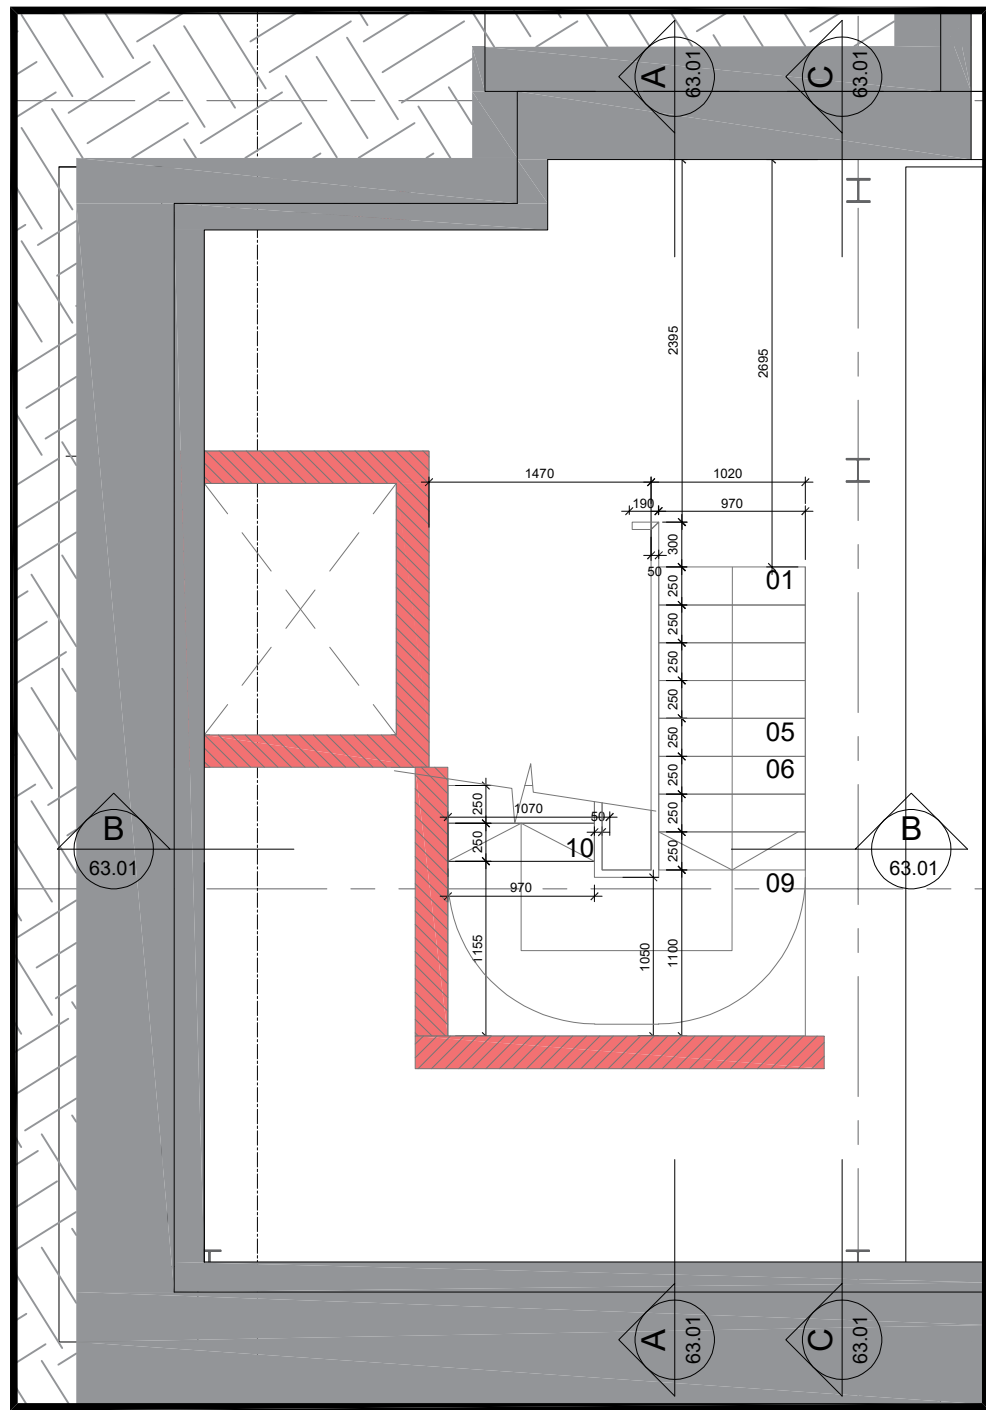


1
63.01

BASEMENT_KEYPLAN
SCALE: 1:50

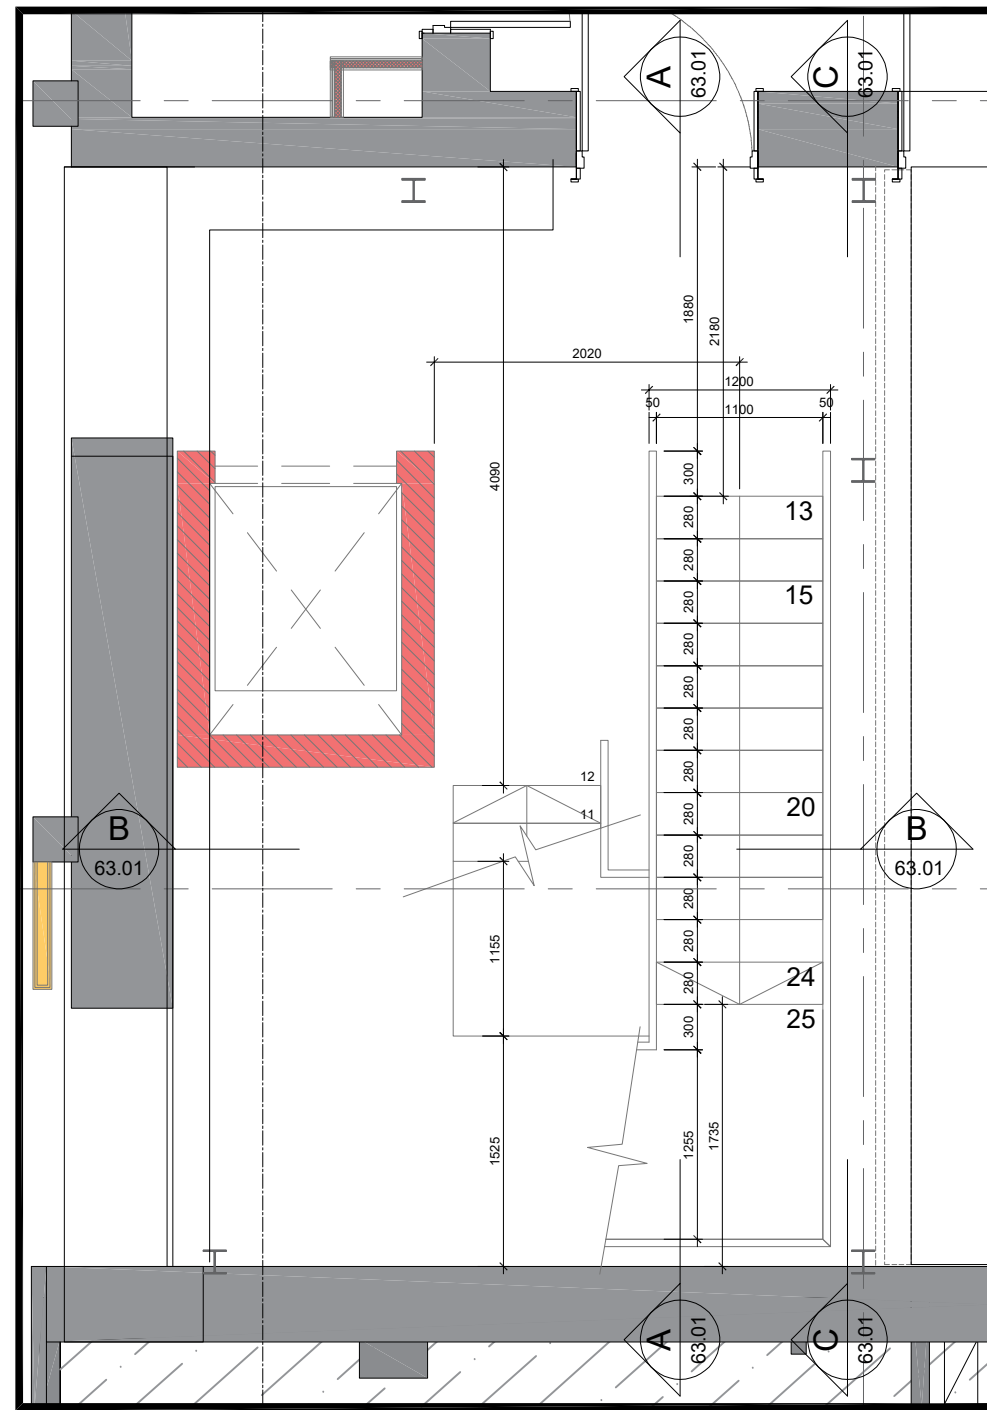


2
63.01

GFL_KEYPLAN
SCALE: 1:50

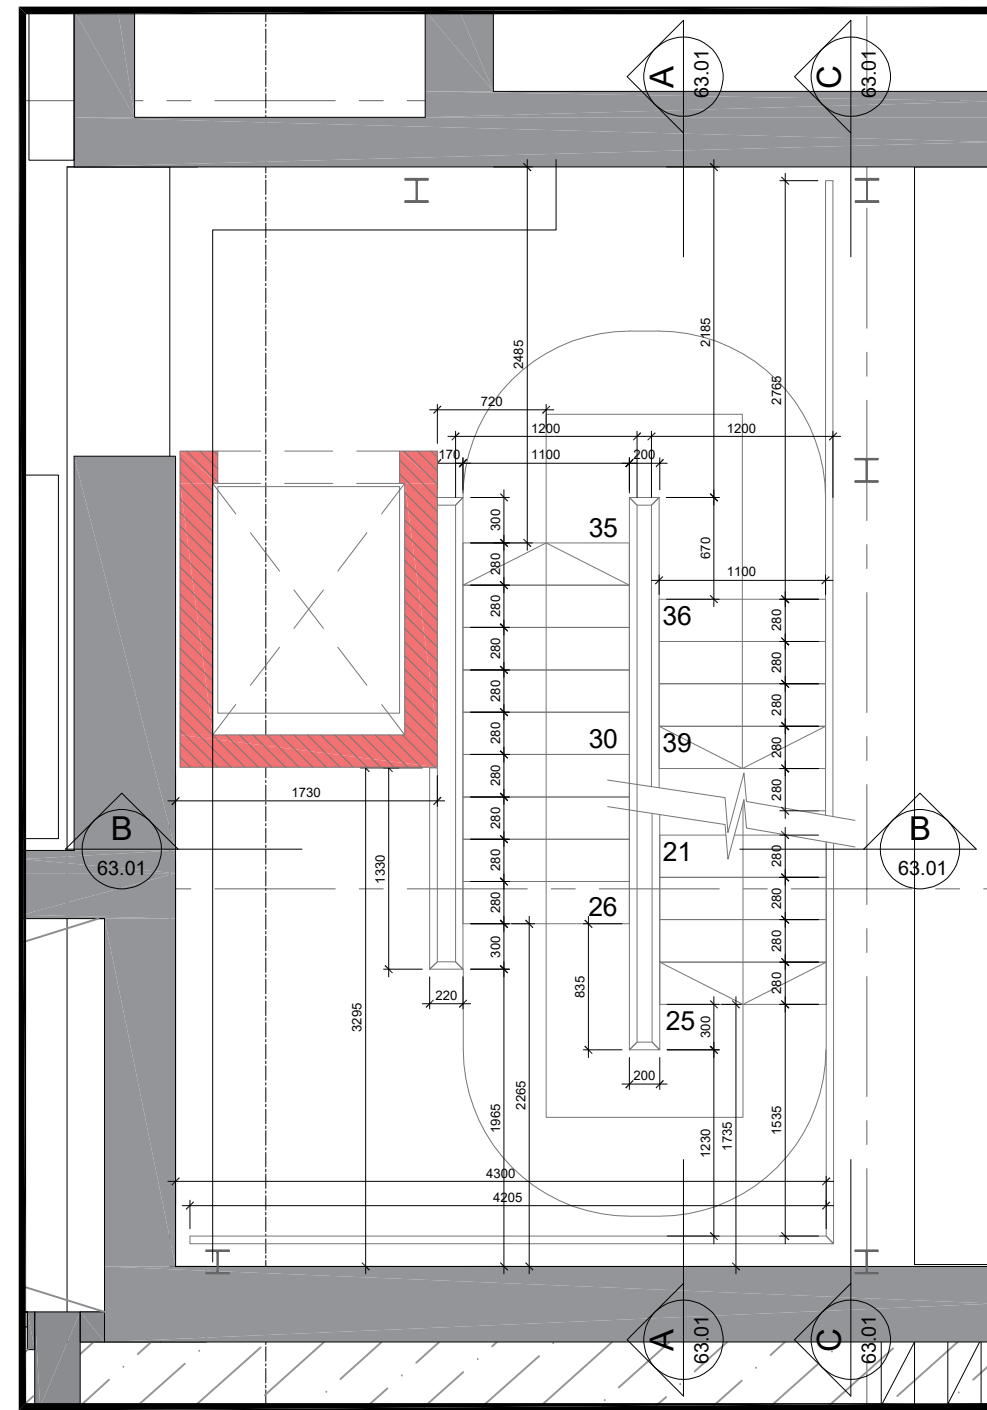


3
63.01

FIRST_FL_KEYPLAN
SCALE: 1:50

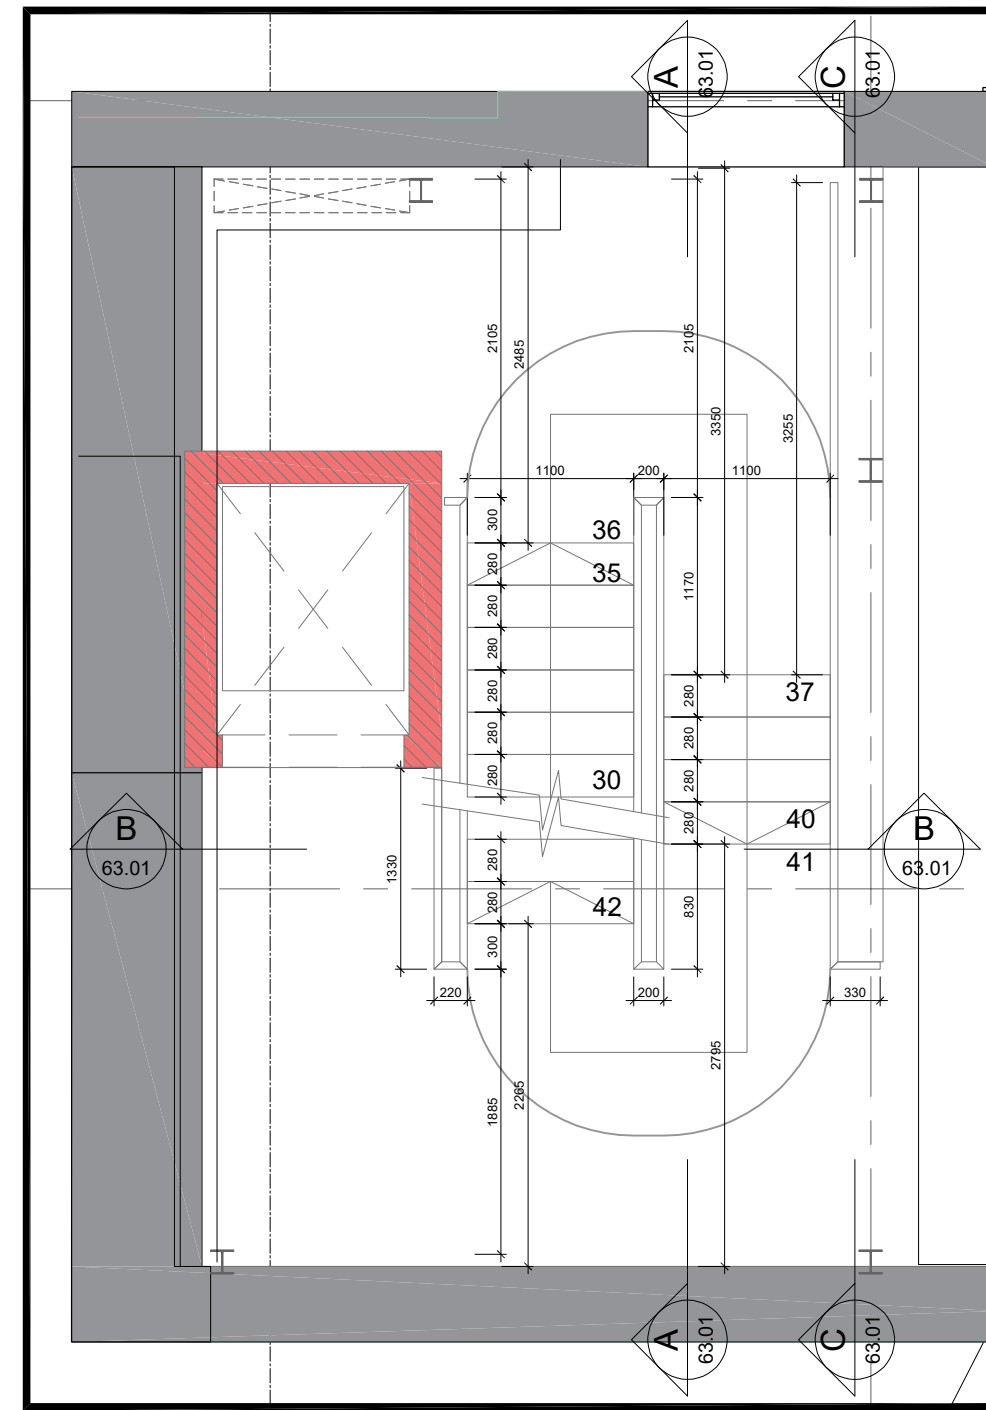

4
63.01

SECOND_FL_KEYPLAN
SCALE: 1:50

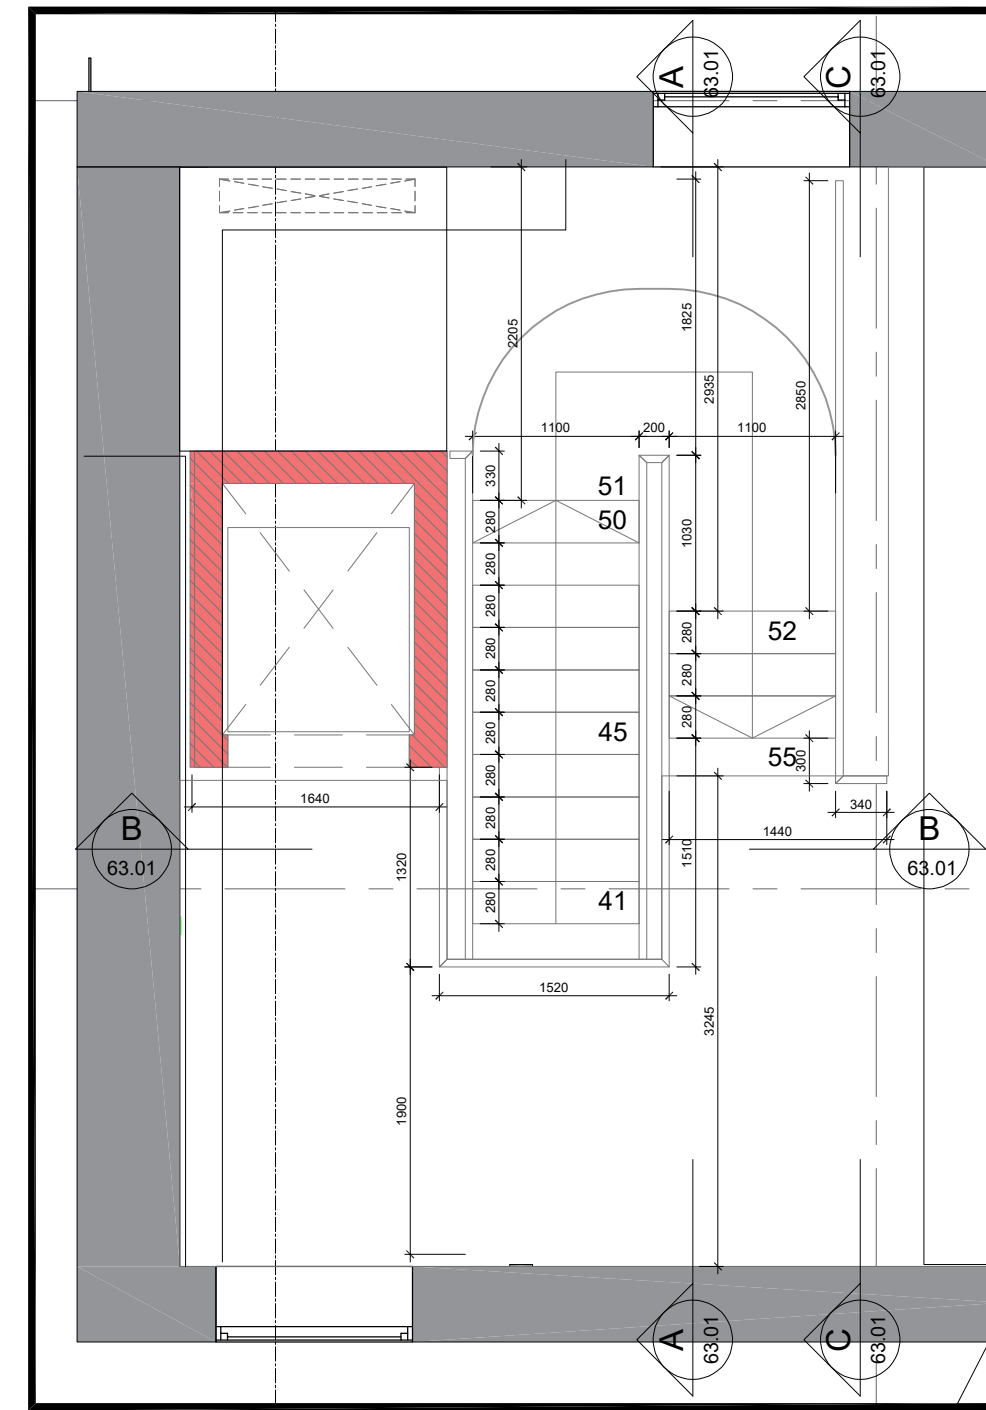

5
63.01

THIRD_FL_KEYPLAN
SCALE: 1:50

A1

Do not scale drawing, work to figured dimensions. All dimensions to be checked on site. Any errors or discrepancies to be reported to MILLIMETRE DESIGN. This drawing may not be edited or modified without permission. This drawing is to be read in colour and in conjunction with all relevant consultant and specialist drawings, schedules and documentation. Only build from drawings issued as Construction.

Legend


- AREA OUTSIDE SCOPE OF WORKS
- INTERIOR ROOM No.
- INTERIOR DOOR No.
- FIXED JOINERY No.
- INTERNAL GLAZED SCREEN No.
- EXTERNAL GLAZING No.
- EXTERNAL DOOR No.
- SET PIECE No.
- 60min FIRE RESISTANCE BLOCKWORK
- 60min FIRE RESISTANCE PARTITION
- 30min FIRE RESISTANCE PARTITION
- NON FIRE RESISTANCE PARTITION
- INSULATED PLASTERBOARD
- 60min / ACOUSTIC INFILL PLASTERBOARD SECTIONS
- 60min SHAFTWALL PLASTERBOARD SECTIONS

Notes:

To be read in conjunction with all relevant drawings & schedules, refer to drawing register for breakdown of drawings.

Drawing to be printed in colour.

NOTE: FINAL LIFT SHAFT SIZE TBC BASED UPON DAC APPLICATION & RECOMMENDATIONS FOR OCCUPANCY.

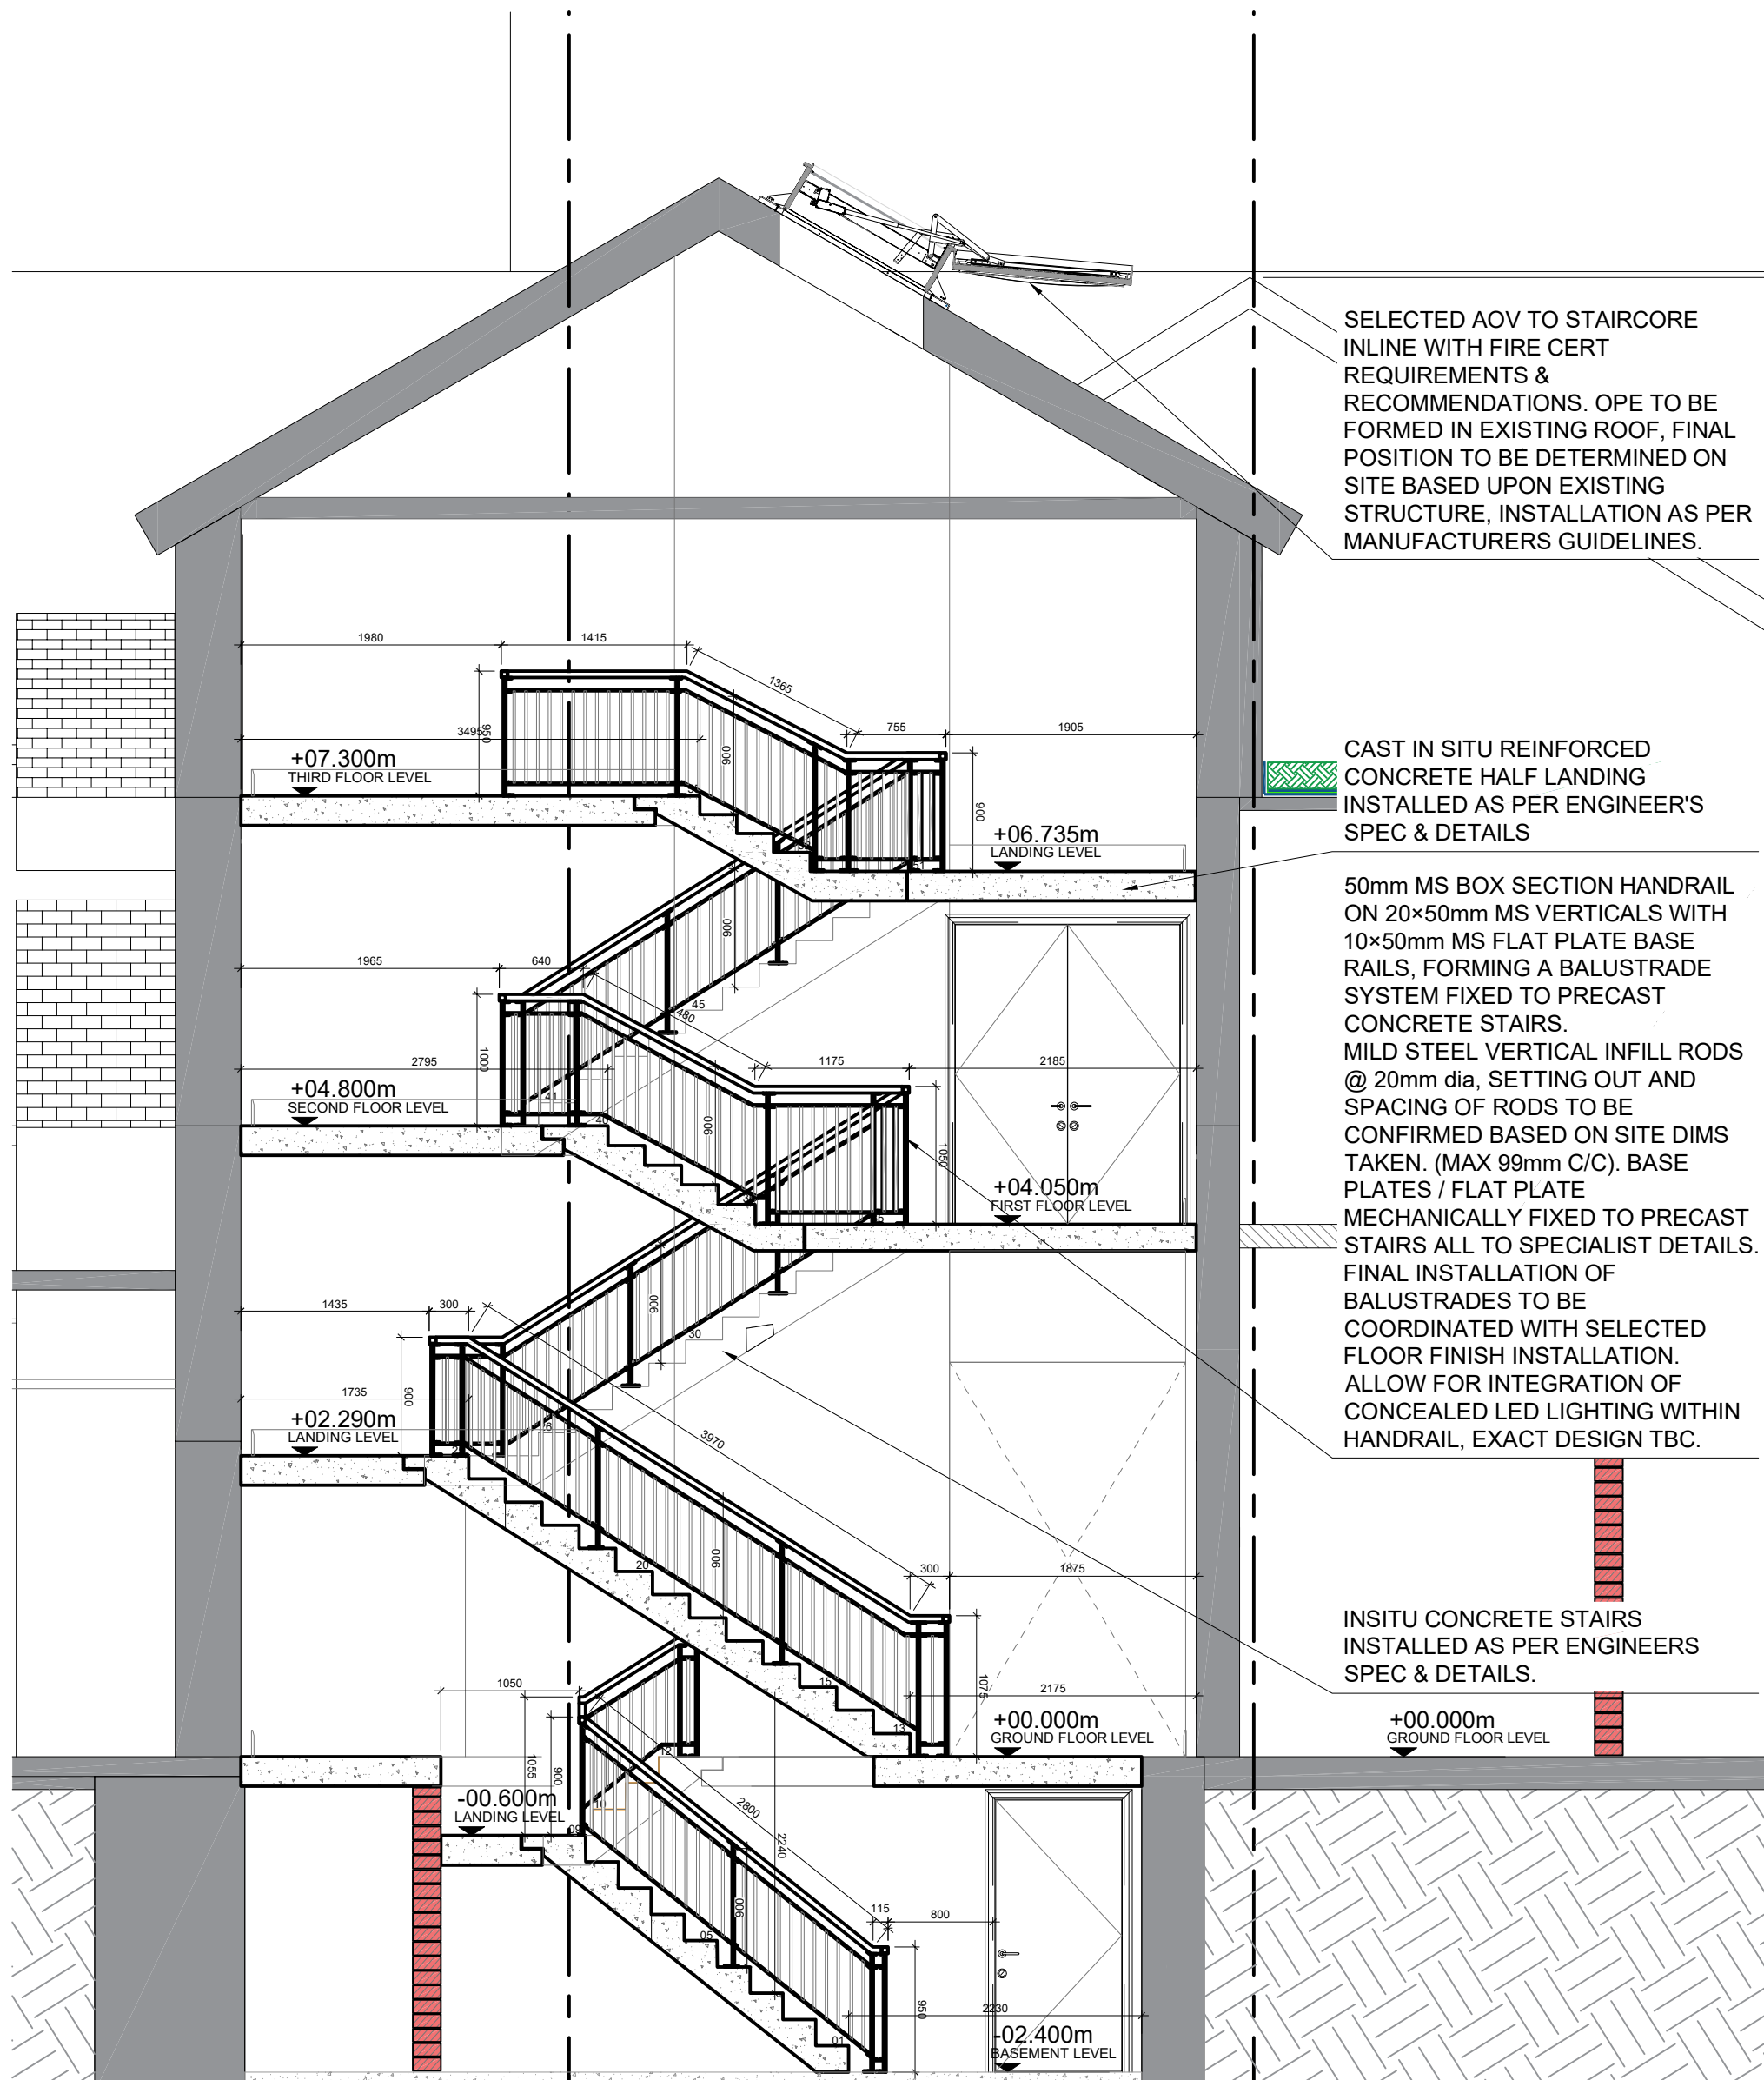

6
63.01


SECTION A-A
SCALE: 1:50

SELECTED AOV TO STAIRCORE IN LINE WITH FIRE CERT REQUIREMENTS & RECOMMENDATIONS. OPE TO BE FORMED IN EXISTING ROOF, FINAL POSITION TO BE DETERMINED ON SITE BASED UPON EXISTING STRUCTURE. INSTALLATION AS PER MANUFACTURERS GUIDELINES.

CAST IN SITU REINFORCED CONCRETE HALF LANDING INSTALLED AS PER ENGINEER'S SPEC & DETAILS


50mm MS BOX SECTION HANDRAIL ON 20x50mm MS VERTICALS WITH 10x50mm MS FLAT PLATE BASE RAILS, FORMING A BALUSTRADE SYSTEM FIXED TO PRECAST CONCRETE STAIRS. MILD STEEL VERTICAL INFILL RODS @ 20mm dia, SETTING OUT AND SPACING OF RODS TO BE CONFIRMED BASED ON SITE DIMS TAKEN, (MAX 90mm C/C). BASE PLATES / FLAT PLATE MECHANICALLY FIXED TO PRECAST STAIRS ALL TO SPECIALIST DETAILS. FINAL INSTALLATION OF BALUSTRADES TO BE COORDINATED WITH SELECTED FLOOR FINISH INSTALLATION. ALLOW FOR INTEGRATION OF CONCEALED LED LIGHTING WITHIN HANDRAIL, EXACT DESIGN TBC.

INSITU CONCRETE STAIRS INSTALLED AS PER ENGINEERS SPEC & DETAILS.

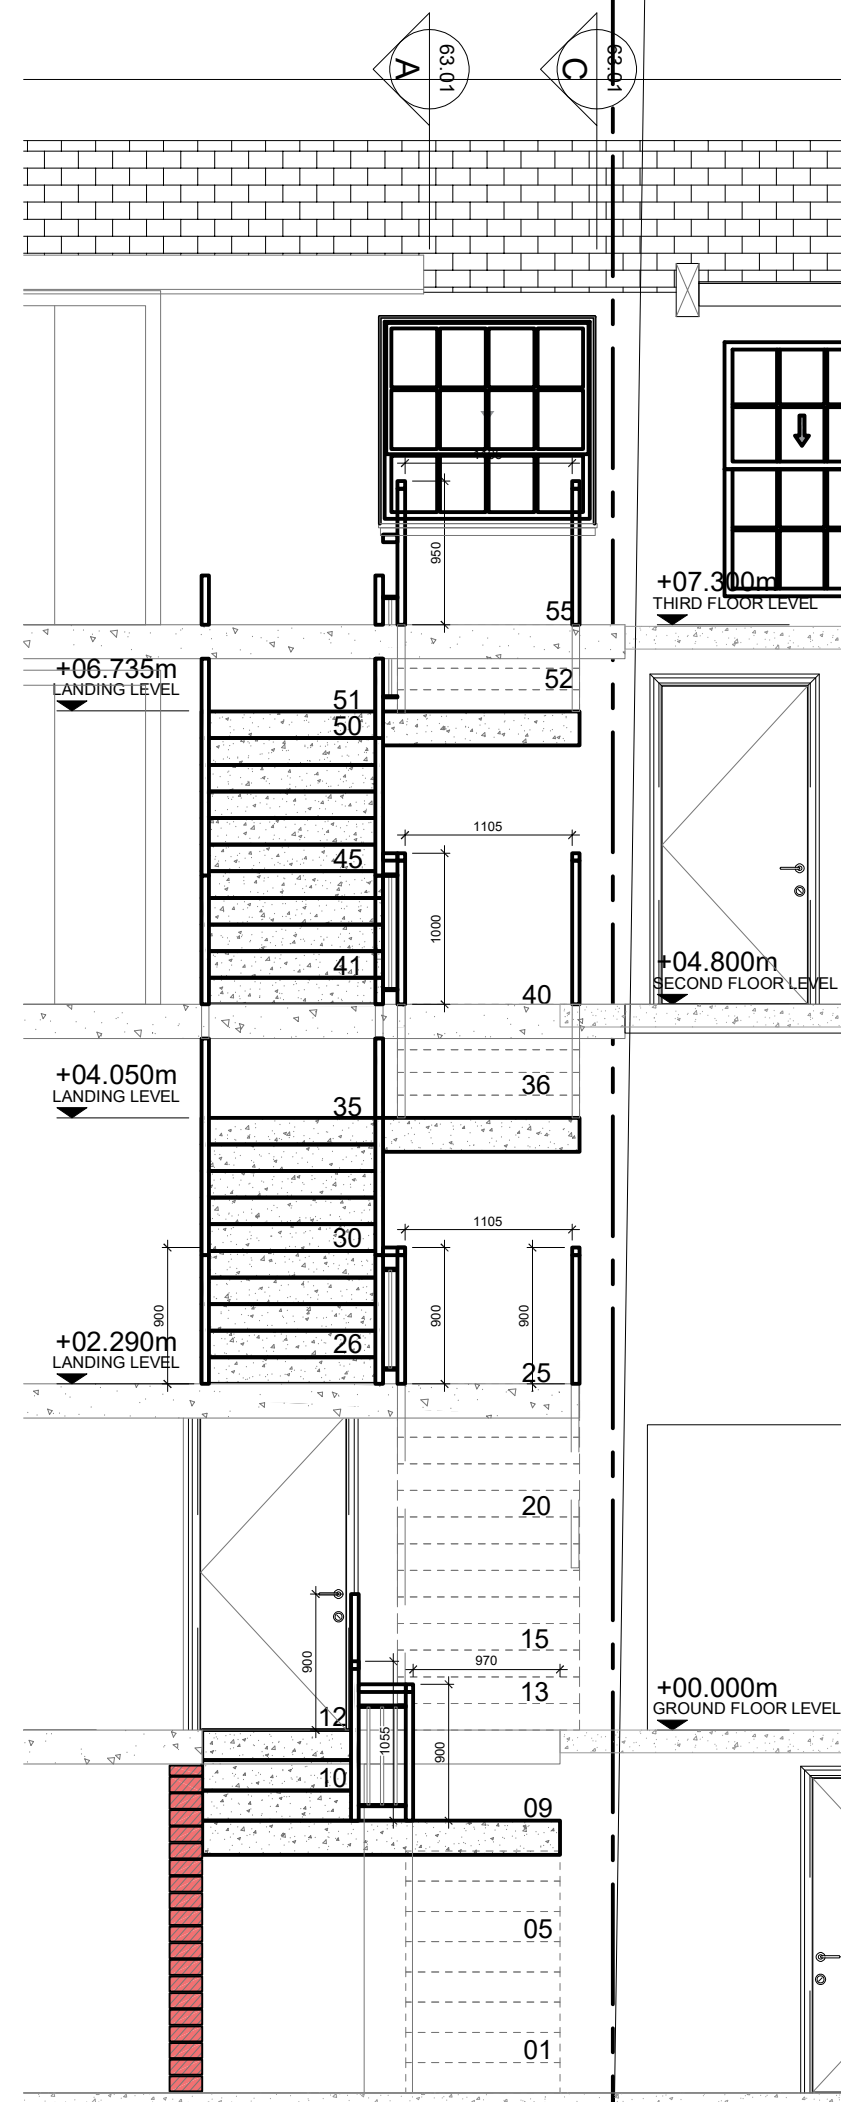


7
63.01

SECTION B-B
SCALE: 1:50

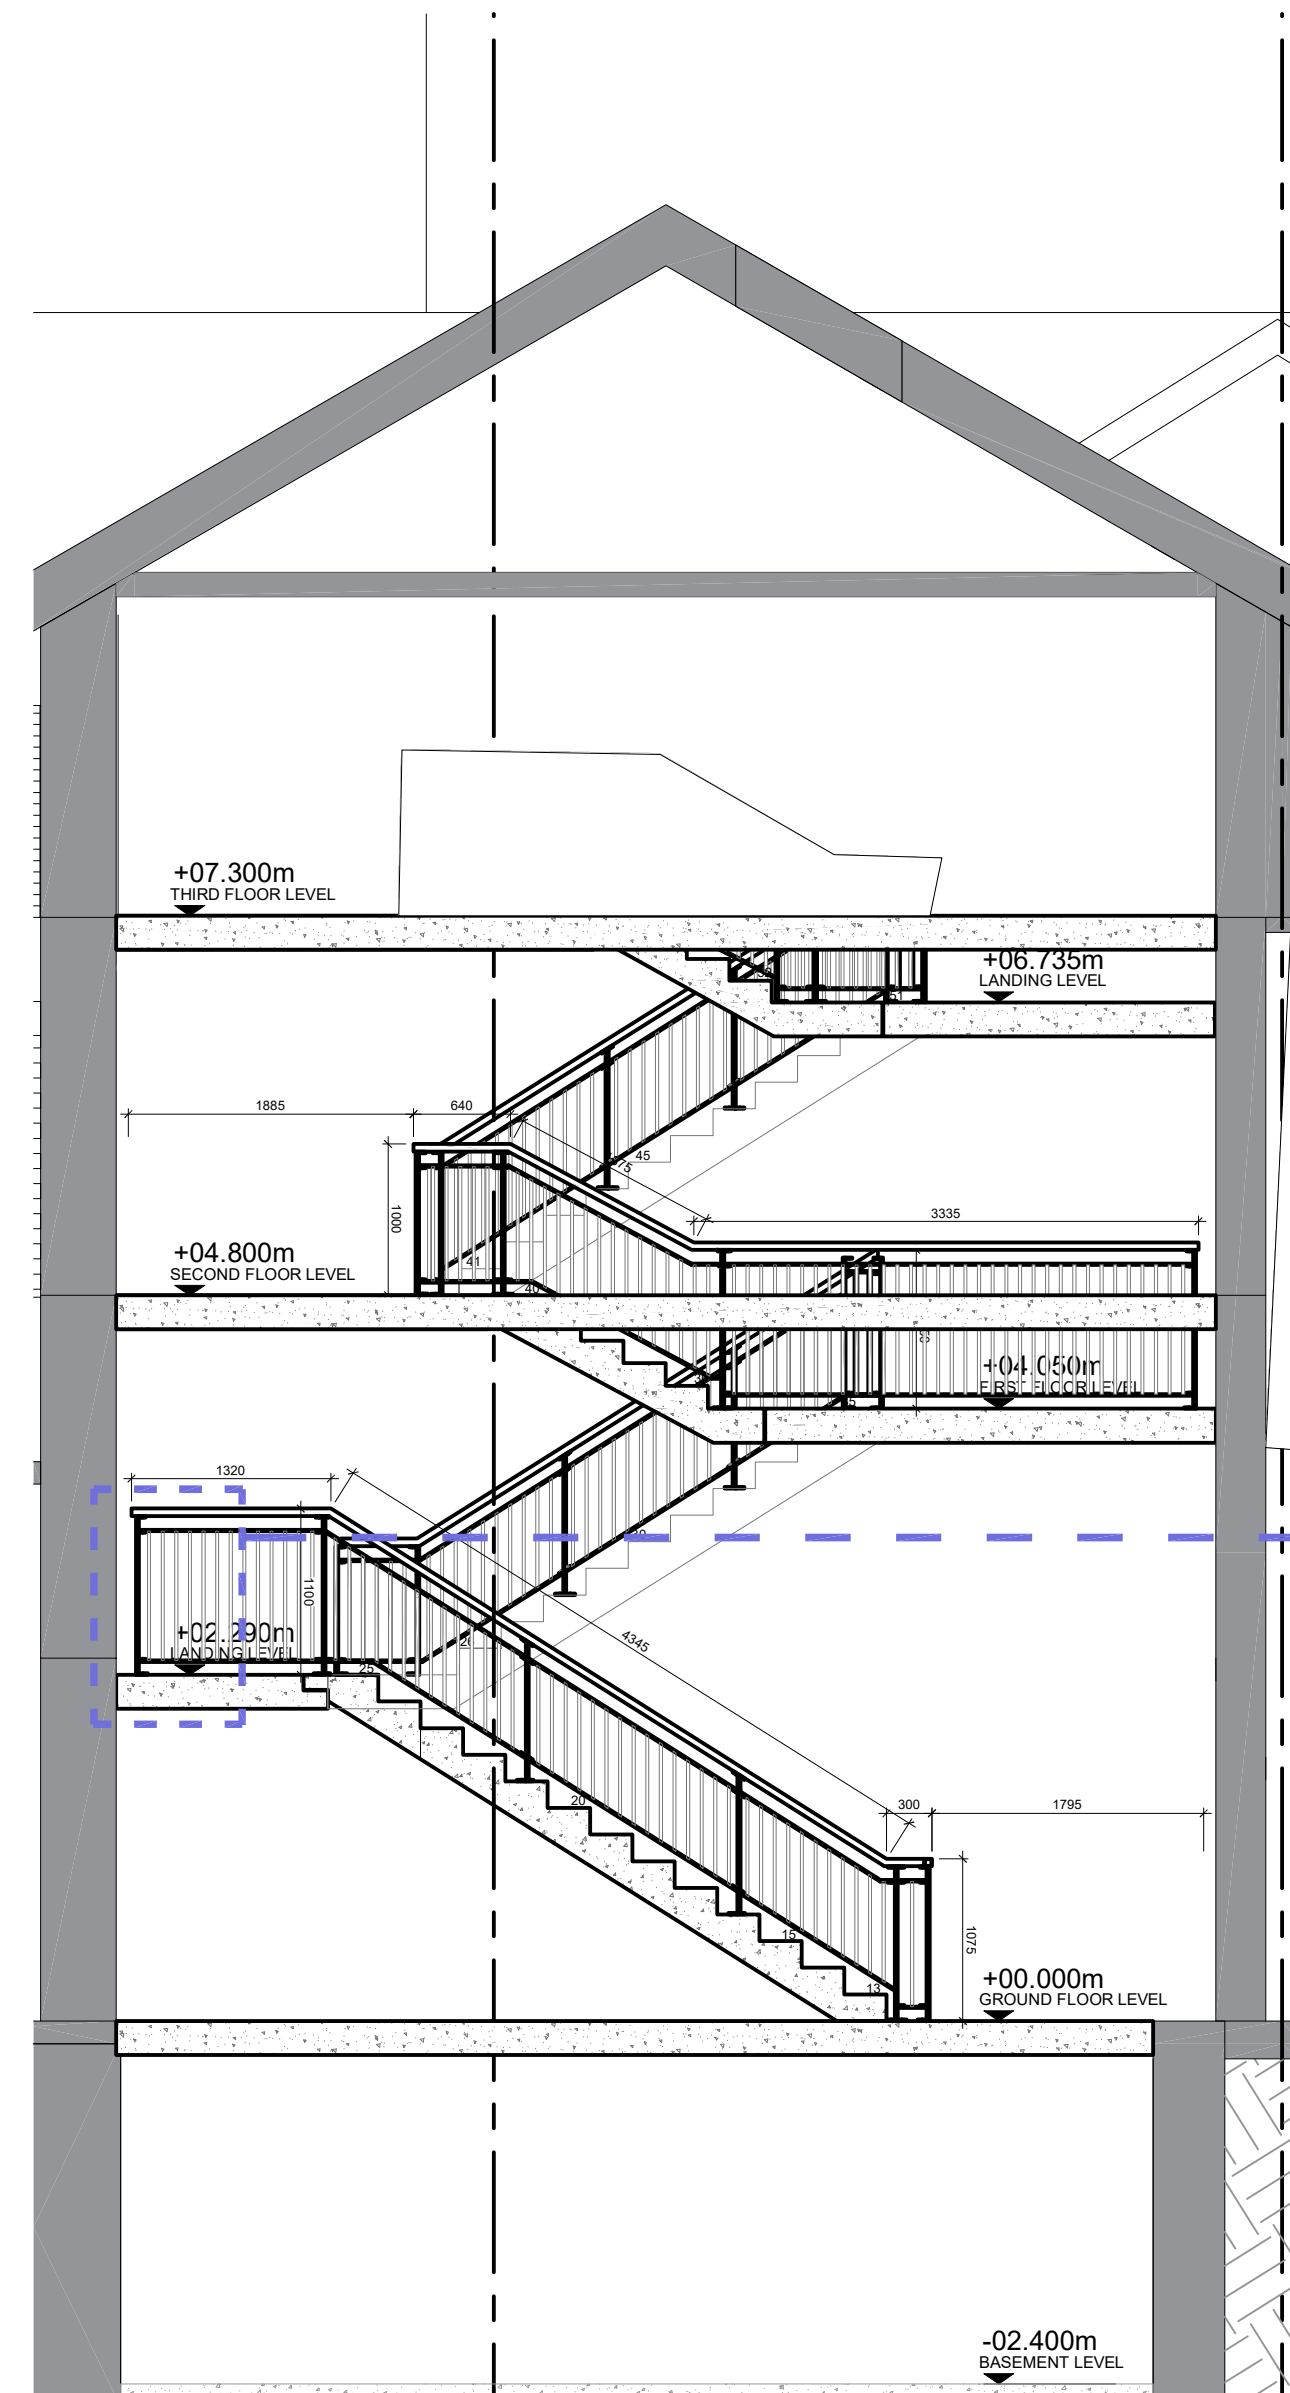


8
63.01

SECTION C-C
SCALE: 1:50

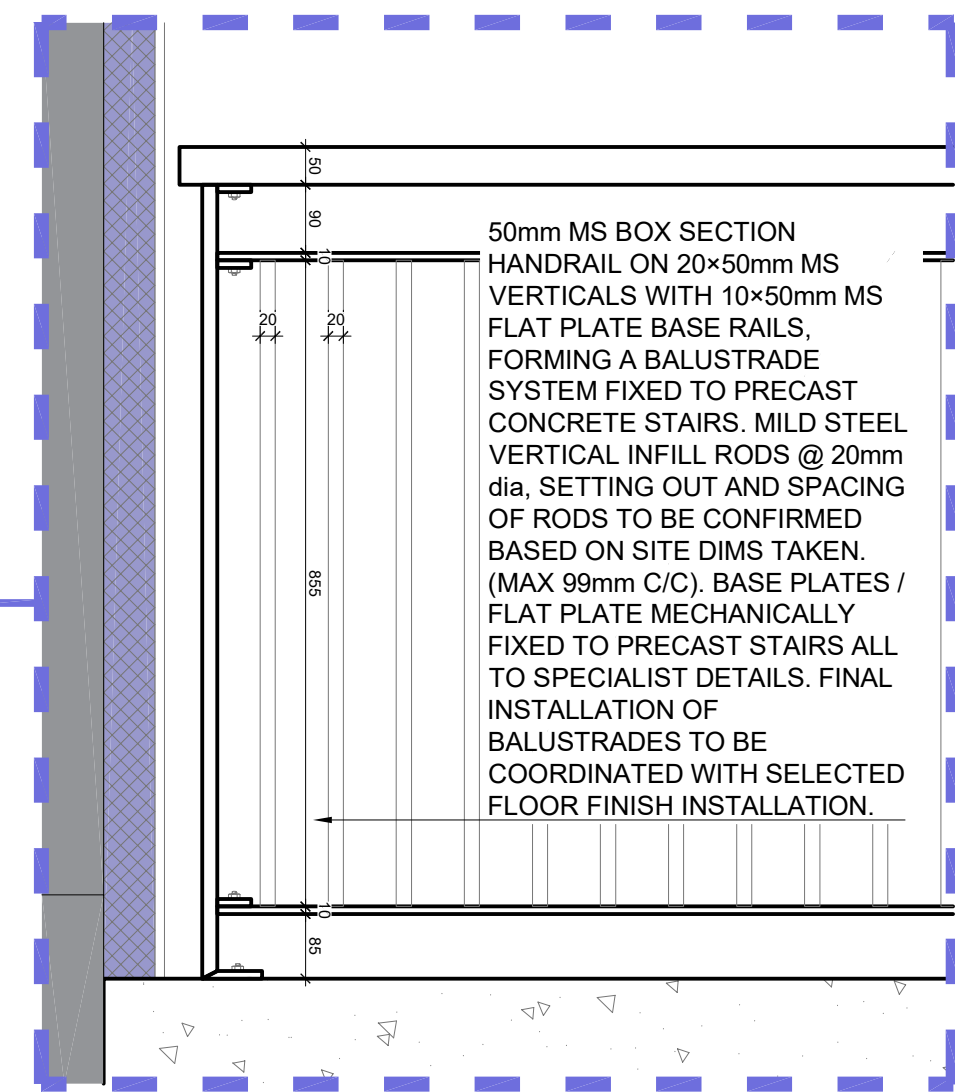

9
63.01

HANDRAIL / BALUSTRADE DETAIL
SCALE: 1:10

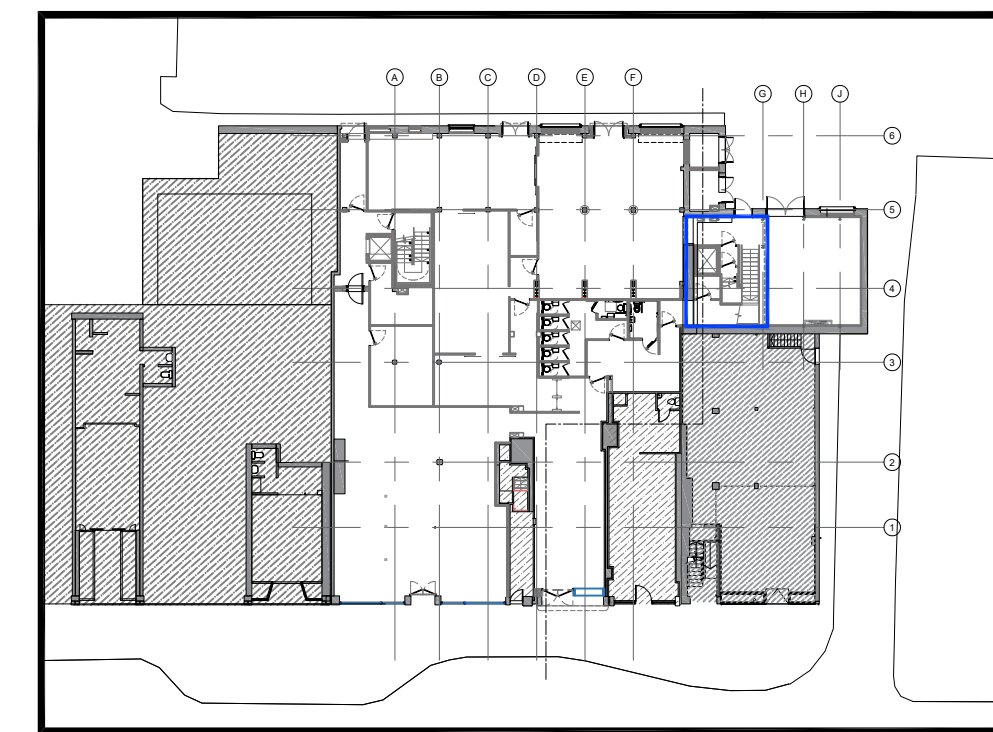

10
63.01

GFL_KEYPLAN
SCALE: NTS

MILLIMETRE DESIGN issues this drawing (and associated Schedules) with the following conditions and understandings: Upon receipt of same, we understand that the recipient accepts these terms and conditions: The information contained herein, where issued for Planning / Tender, must not be used for the coordination and/or construction of this project. Only build from drawings issued as 'Construction'. MILLIMETRE DESIGN does not take responsibility for information scaled off drawings, any measurements taken from information that is not dimensioned, is at the risk of the recipient. All dimensions must be checked on site. Any errors or discrepancies herein or within associated documents, to be reported to MILLIMETRE DESIGN immediately. The recipient is responsible for checking that the information as issued herein is correct and complete, by consulting with all other information as issued as part of this package and during the course of the project, inclusive of checking all dimensions on site. This drawing is to be read in colour and in conjunction with all relevant consultant and specialist drawings, schedules and documentation (both hard copy and for soft copy information issued). MILLIMETRE DESIGN accepts no liability or responsibility for any loss or damage suffered by the recipient, arising out of, or in connection with, the use or misuse of the information issued or contained herein or within the associated schedules as issued as part of this pack. The original documents and their copyright, remain the property of MILLIMETRE DESIGN. The information contained herein is changed in any way, all references to MILLIMETRE DESIGN must be removed and the total responsibility thereof of said alterations / additions, become that of the person/company/contractor making those changes or additions. Compliance with all Building Regulations, Fire Safety Certificate Approvals, Disabled Access Certificate approvals, and Planning Permission approvals, is the responsibility of the Building Contractor. All information is issued on the express understanding that the recipient accepts these limitations and disclaimers. The terms 'document' and 'information' in the above, refers to both text documents and drawings in either 'hard copy or electronic format'.