


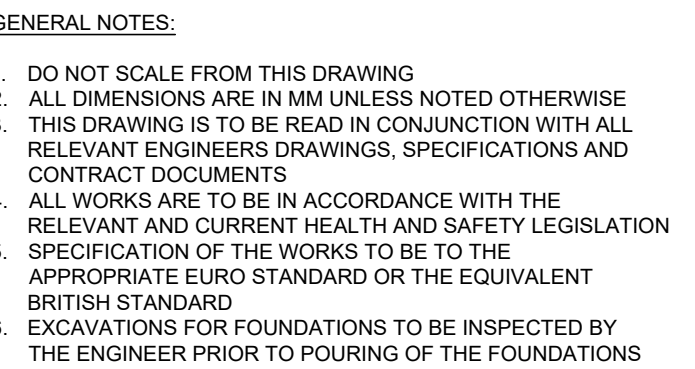

KEY TO SYMBOLS AND ABBREVIATIONS:	
TOC	STRUCTURAL FLOOR LEVEL
TOT	TOP LEVEL OF STRUCTURAL CONCRETE
TOS	TOP LEVEL OF STEEL BEAM/COLUMN
FFI	FINISHED FLOOR LEVEL
RO	REINFORCED CONCRETE
BM	PRE-CAST
COL	BEAM/S
CONC.	COLUMN/S
-----	CONCRETE
-----	GRID LINE / CENTRE LINE
IJ	ISOLATION JOINT
LJ	LONGITUDINAL JOINT
TJ	TRANSVERSE JOINT
MJ	MOVEMENT JOINT
TL	TOP LEVEL
THK	THICK
HDG	HOT DIPPED GALVANIZED

LEGEND:

	DEMOLITION EXISTING BLOCK WALL 215mm
	DEMOLITION EXISTING STONE WALL 500-600mm
	ex 215mm SOLID 7.5N BLOCKWORK WALL
	ex stonework

	DETAILED SECTION 1-1 SHOW ON DRG. T4988-S002
	MEANS REFER TO DRAWING T4988-S003 FOR DETAIL ENLARGED DETAIL '1'

MEMBER LEGEND

STEEL S275 JO UNO

C1 203x133ub

C2 152x127RSJ37 with
350x350 rc surround

C3 203uc46

C4 254uc73

C5 350x700 RC column

C6 350x1150 RC column

C7 305uc97

C8 152uc37 (S355)

C9 152uc44 (S355)

-	CF	CF	TENDER ISSUE	28.04.26
REV	REV BY	APPRD	DESCRIPTION	DATE

**JA
Gorman**
consulting engineers
project managers

Forest Park,
Mullingar, Co. Westmeath.
Tel: 044-9347338 / 9347341
Fax: 044-9347400
Email: info@jagorman.ie
Web: www.jagorman.ie

CLIENT: CARROLLS IRISH GIFTS

PROJECT TITLE:

IMMERSIVE EXPERIENCE
TALBOT STREET DUBLIN

DRAWING TITLE:

**BASEMENT PLAN
DEMOLITIONS & TEMPORARY
WORKS**

LOT SIZE: A1	PLOT SCALE: 1:75	DRAWN BY: CF	CHECKED BY: CF
APPROVED BY: JG	PROJECT No: 4988	DRAWING No: T4988-S002	REV: -