


Scope

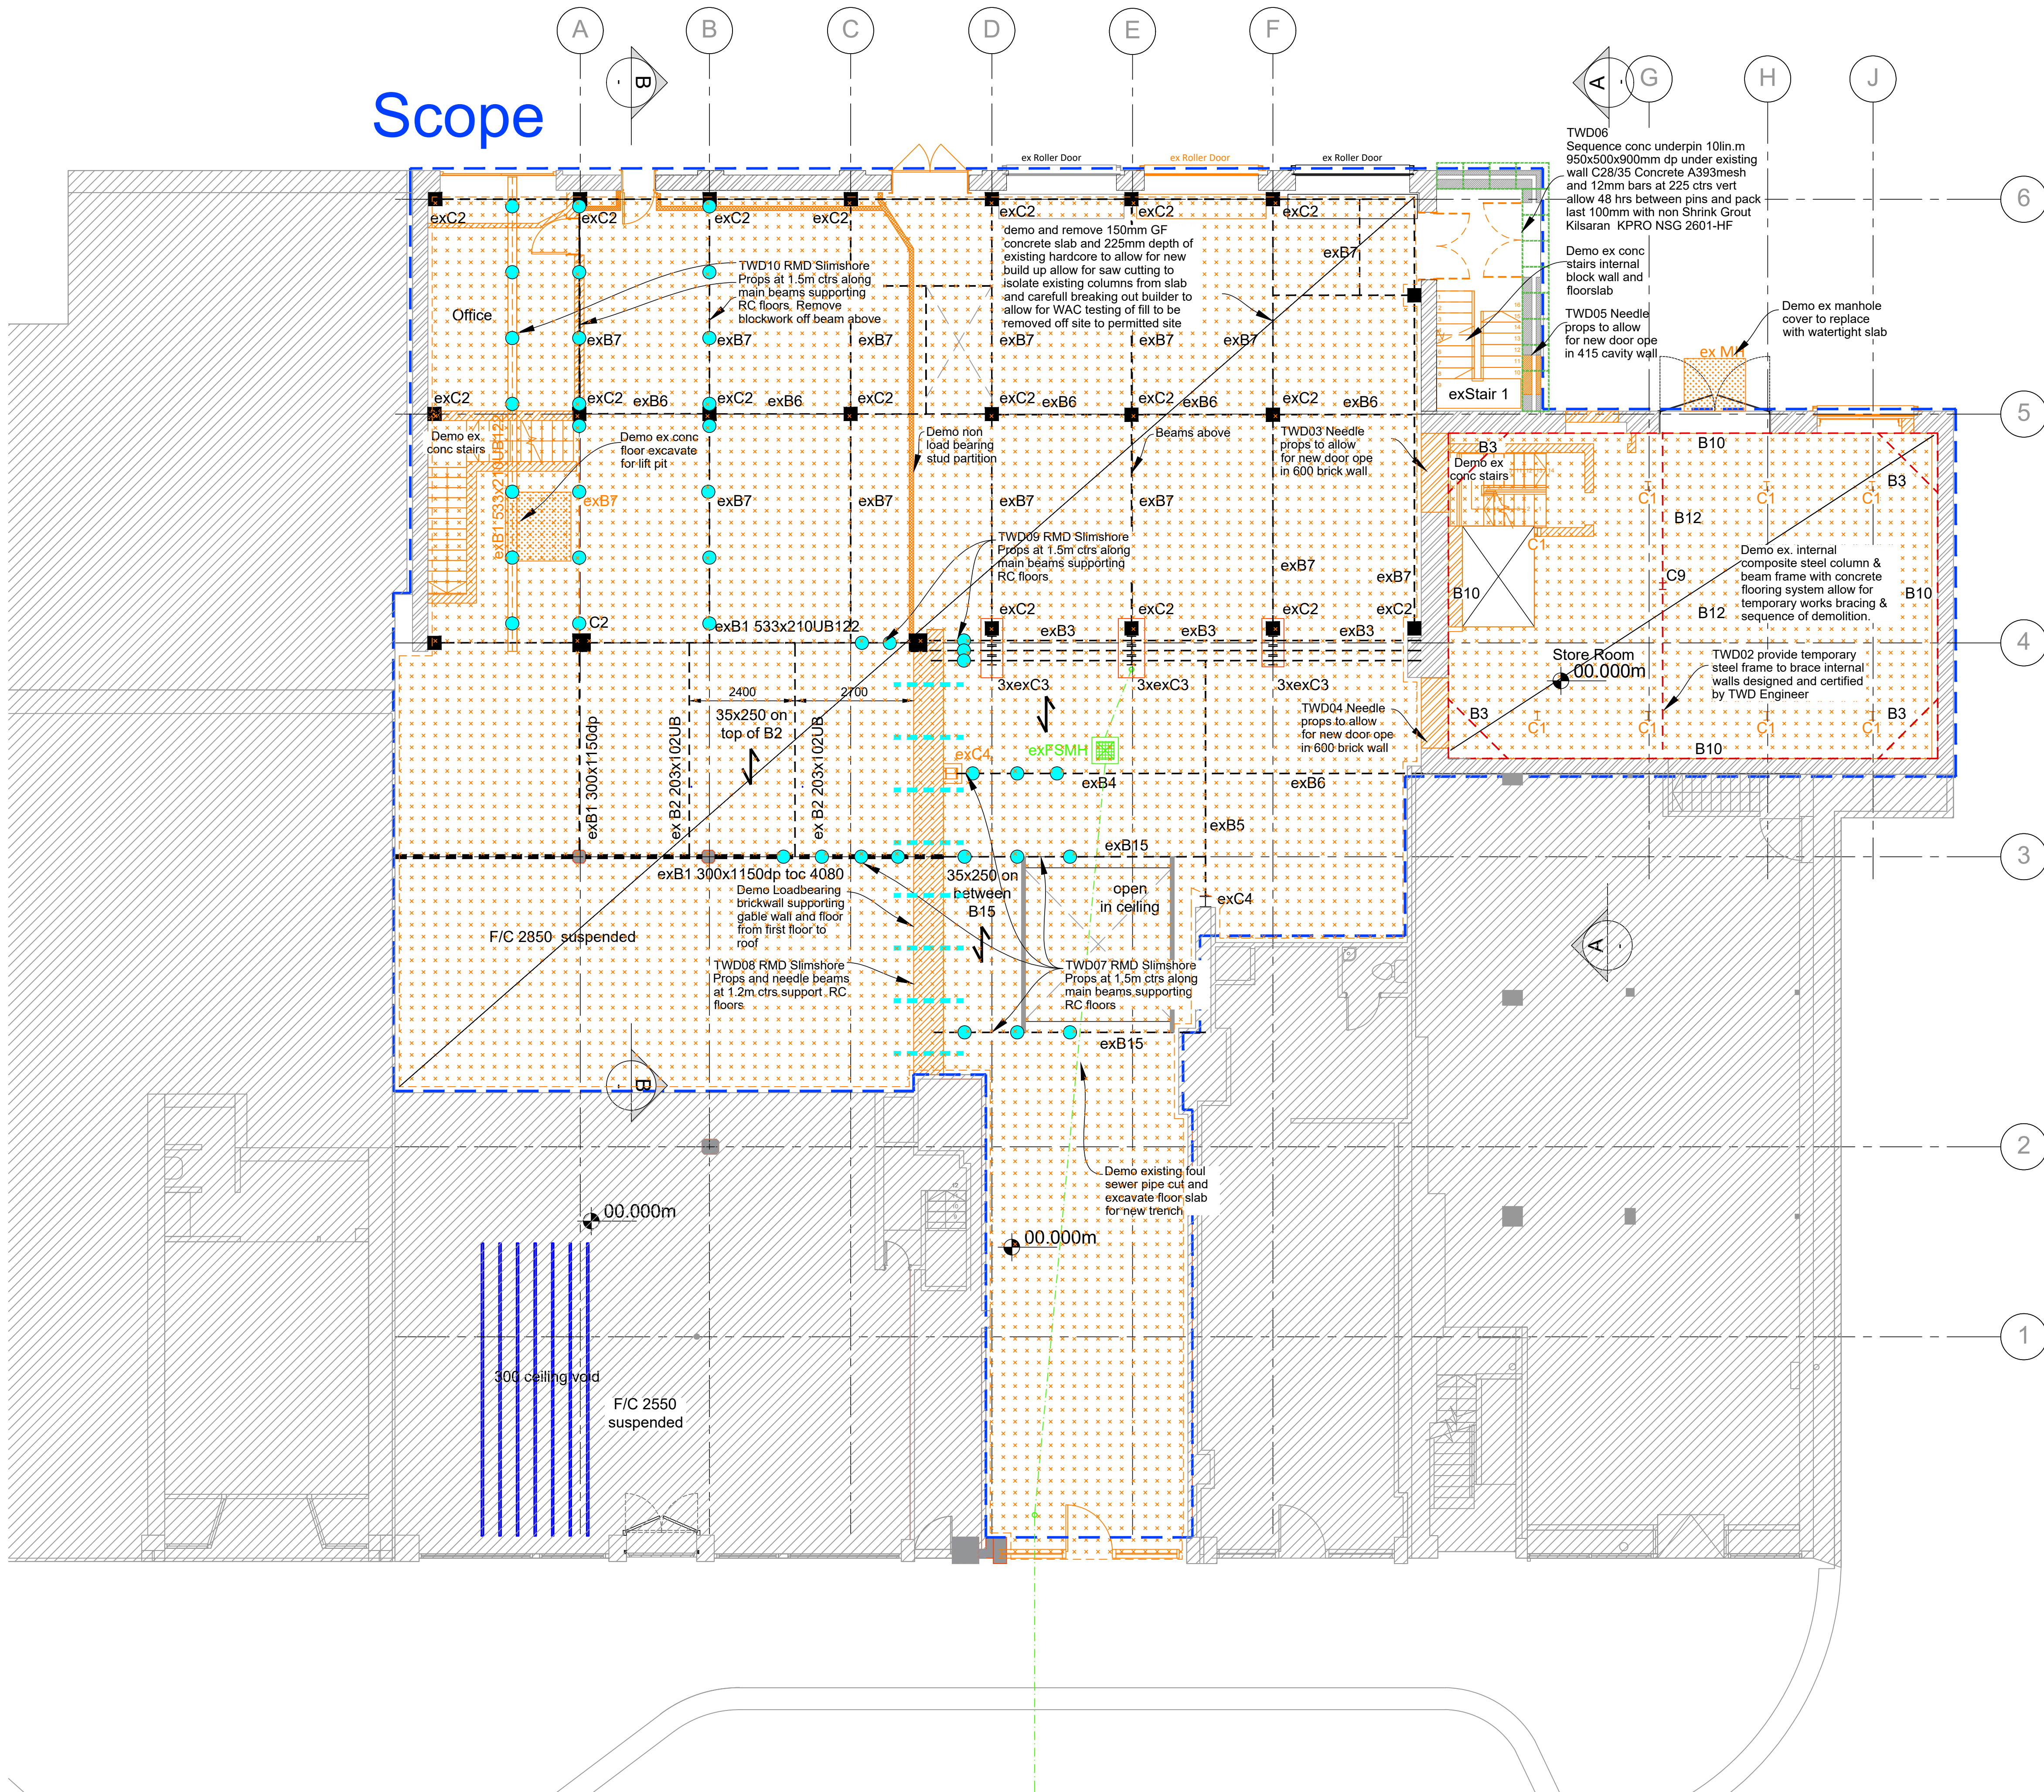

- GENERAL NOTES:
- DO NOT SCALE FROM THIS DRAWING
 - ALL DIMENSIONS ARE IN MM UNLESS NOTED OTHERWISE
 - THIS DRAWING IS TO BE READ IN CONJUNCTION WITH ALL RELEVANT ENGINEERS DRAWINGS, SPECIFICATIONS AND CONTRACT DOCUMENTS
 - ALL WORKS ARE TO BE IN ACCORDANCE WITH THE RELEVANT AND CURRENT HEALTH AND SAFETY LEGISLATION
 - SPECIFICATION OF THE WORKS TO BE TO THE APPROPRIATE EURO STANDARD OR THE EQUIVALENT BRITISH STANDARD
 - EXCAVATIONS FOR FOUNDATIONS TO BE INSPECTED BY THE ENGINEER PRIOR TO POURING OF THE FOUNDATIONS

KEY TO SYMBOLS AND ABBREVIATIONS:	
TOC	STRUCTURAL FLOOR LEVEL
TOS	TOP LEVEL OF STRUCTURAL CONCRETE
FFL	FINISHED FLOOR LEVEL
RC	REINFORCED CONCRETE
PC	PRE-CAST
BM	BEAMS
COL	COLUMNS
CONC.	CONCRETE
U	GRID LINE / CENTRE LINE
LJ	ISOLATION JOINT
TJ	LONGITUDINAL JOINT
MJ	TRANSVERSE JOINT
T.L.	MOVEMENT JOINT
THK	TOP LEVEL
HDK	THICK
HDK	HOT DIPPED GALVANIZED

LEGEND:	
	DEMOLITION EXISTING BLOCK WALL 215mm
	DEMOLITION EXISTING STONE WALL 500-600mm
	ex 215mm SOLID 7.5N BLOCKWORK WALL
	ex stonework
	DETAILED SECTION 1-1 SHOW ON DRG. T4988-S002
	MEANS REFER TO DRAWING T4988-S003 FOR DETAIL ENLARGED DETAIL '1'

MEMBER LEGEND	
STEEL S275 JO UNO	
C1	203x133ub
C2	152x127RSJ37 with 350x350 rc surround
C3	203uc46
C4	254uc73
C5	350x700 RC column
C6	350x1150 RC column
C7	305uc97
C8	152uc37 (S355)
C9	152uc44 (S355)
B1	533x210ub122
B2	203x102ub
B3	203uc52
B4	305uc97
B5	305uc118
B6	152x127RSJ37 with 350x350 rc surround
B7	203x152RSJ52 300x600dp rc
B8	178x102ub19 with 12mm x200 BTM Plate stitch welded
B9	178x102ub19
B10	200x90pfc
B11	230x90pfc30
B12	203uc60
B13	305uc118
B14	305x165ub60
B15	254uc73

REV	CF	CF	TENDER ISSUE	28.04.26
REV	REV	BY	APPROD	DESCRIPTION

TENDER ISSUE

JA Gorman
consulting engineers
project managers

Forest Park,
Mullingar, Co. Westmeath.
Tel: 044-9347338 / 9347341
Fax: 044-9347400
Email: info@jagorman.ie
Web: www.jagorman.ie

CLIENT: **CARROLLS IRISH GIFTS**

PROJECT TITLE: **IMMERSIVE EXPERIENCE TALBOT STREET DUBLIN**

DRAWING TITLE: **GROUND FLOOR PLAN DEMOLITIONS & TEMPORARY WORKS**

PLOT SIZE: A1	PLOT SCALE: 1:75	DRAWN BY: CF	CHECKED BY: CF
APPROVED BY: JG	PROJECT No: 4988	DRAWING No: T4988-S003	REV: -