


Scope

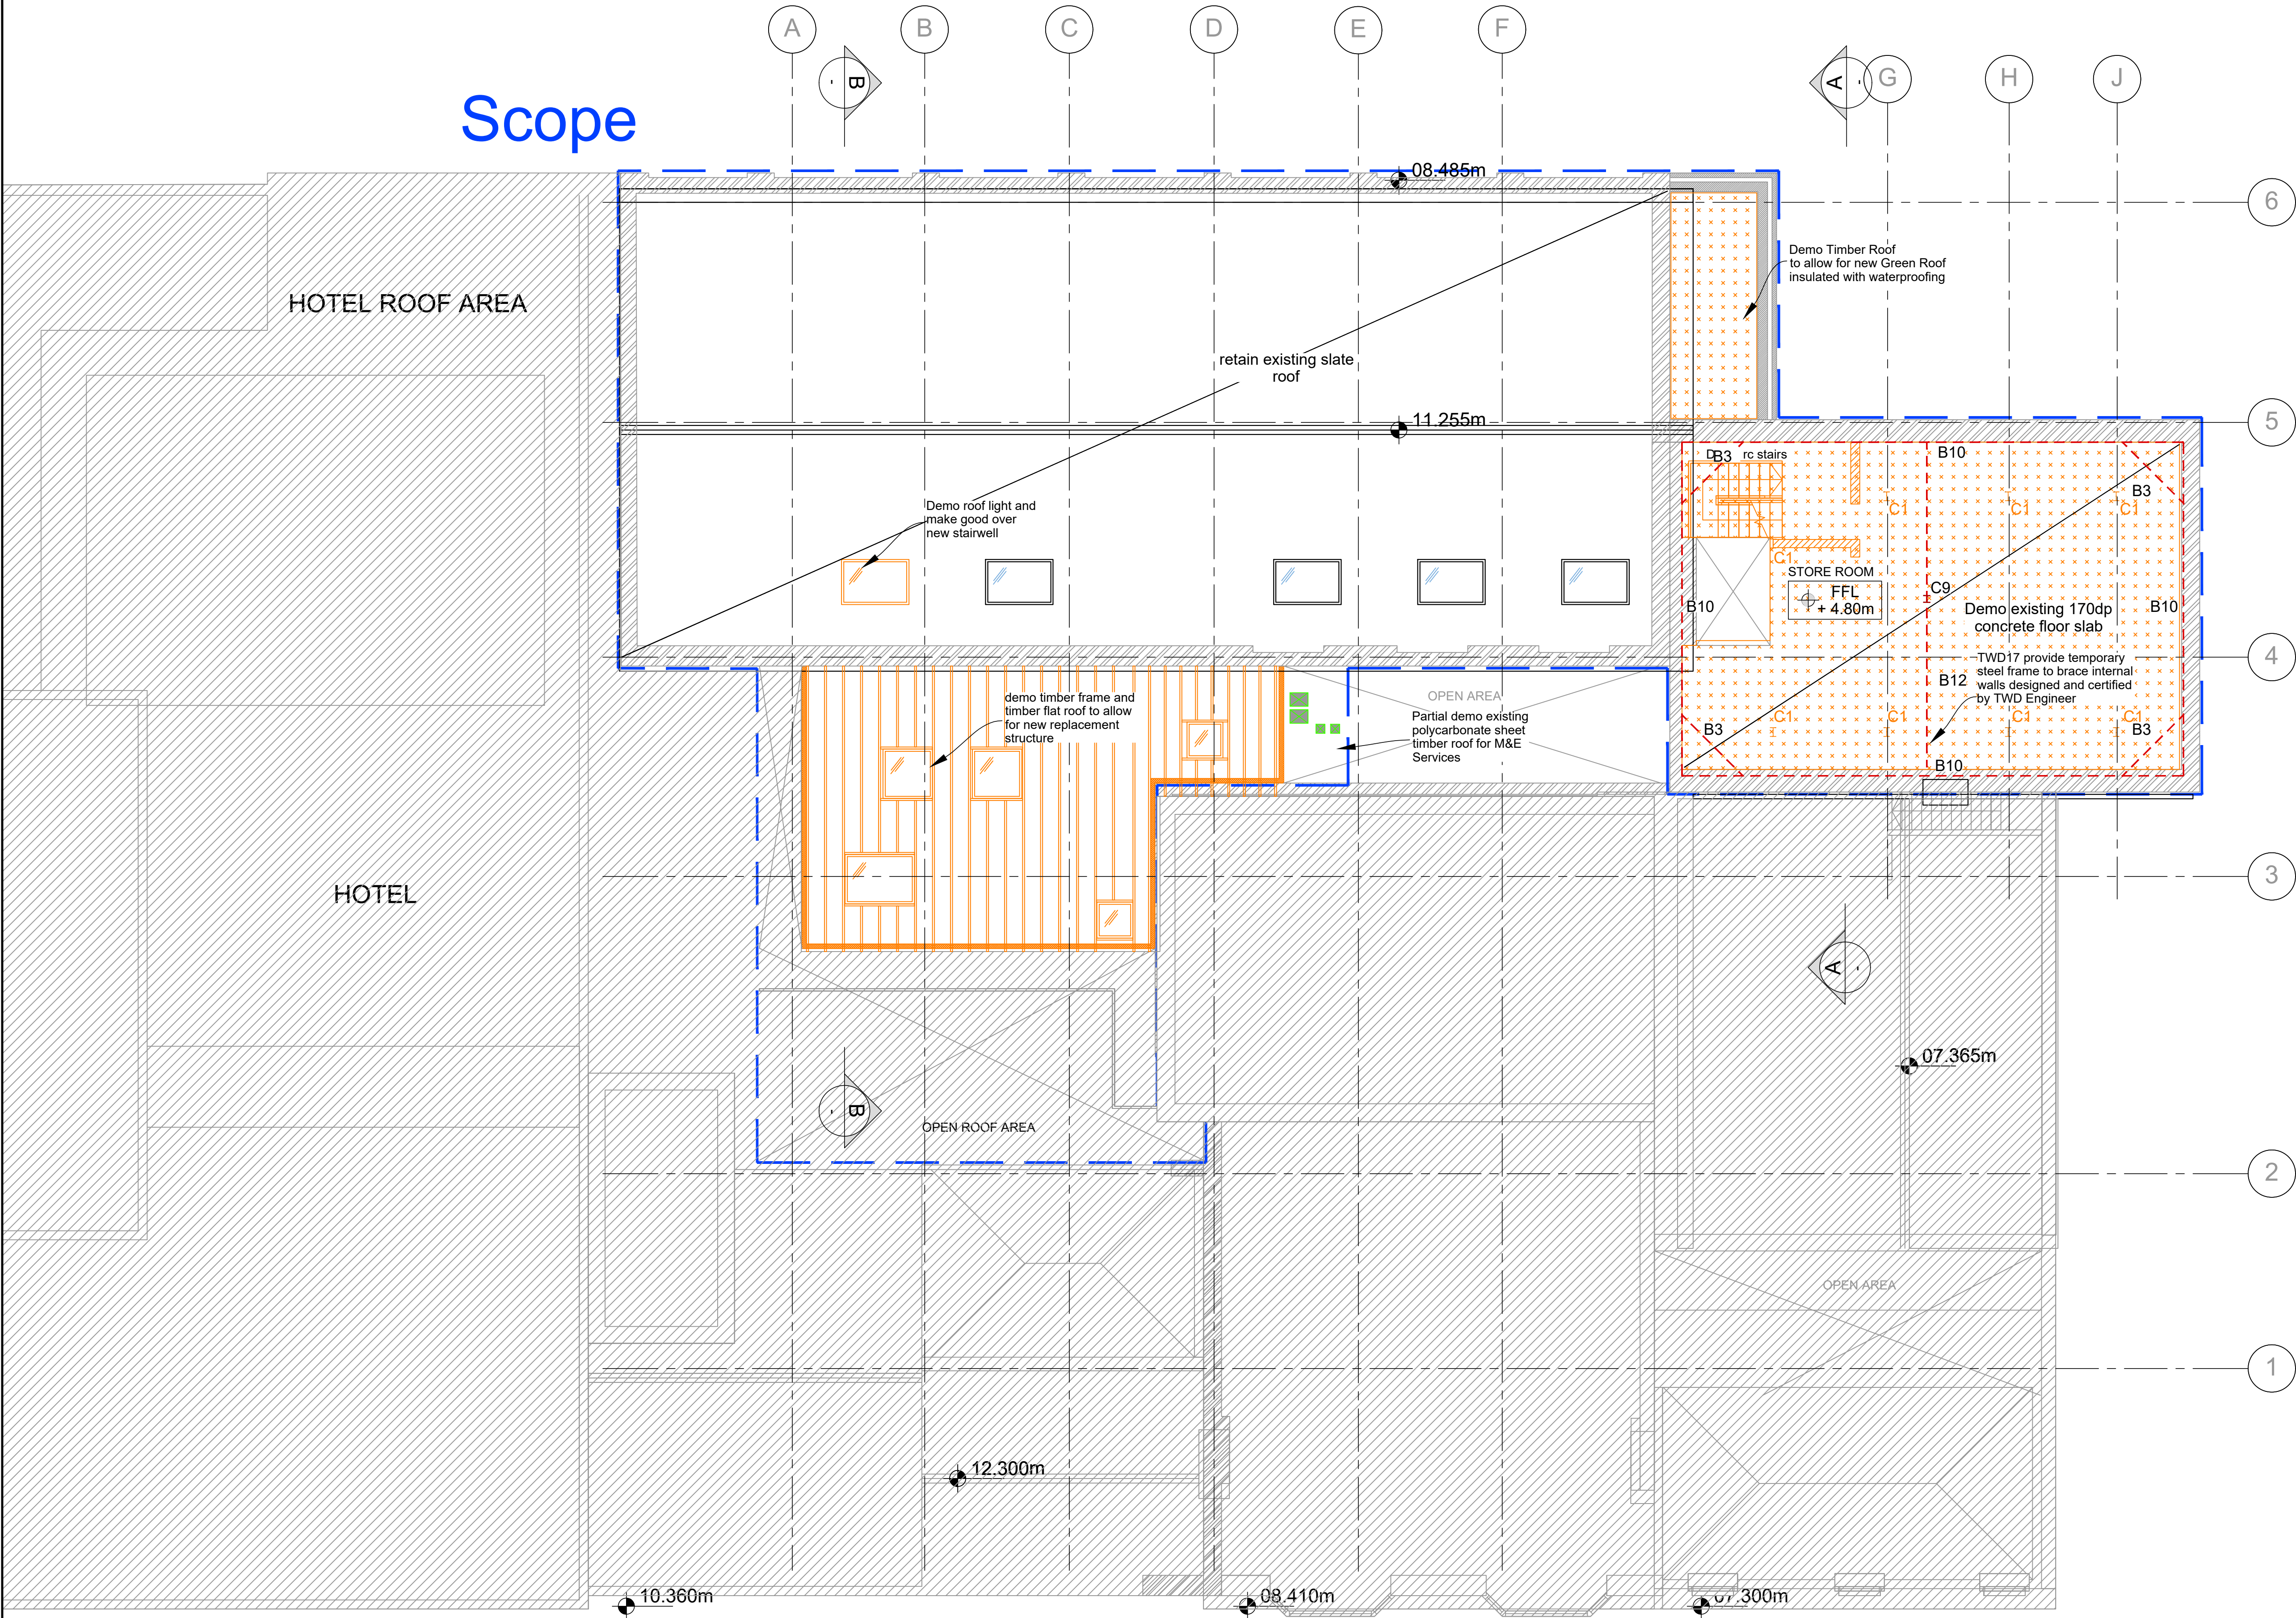

- GENERAL NOTES:
- DO NOT SCALE FROM THIS DRAWING
 - ALL DIMENSIONS ARE IN MM UNLESS NOTED OTHERWISE
 - THIS DRAWING IS TO BE READ IN CONJUNCTION WITH ALL RELEVANT ENGINEERS DRAWINGS, SPECIFICATIONS AND CONTRACT DOCUMENTS
 - ALL WORKS ARE TO BE IN ACCORDANCE WITH THE RELEVANT AND CURRENT HEALTH AND SAFETY LEGISLATION
 - SPECIFICATION OF THE WORKS TO BE TO THE APPROPRIATE EURO STANDARD OR THE EQUIVALENT BRITISH STANDARD
 - EXCAVATIONS FOR FOUNDATIONS TO BE INSPECTED BY THE ENGINEER PRIOR TO POURING OF THE FOUNDATIONS

KEY TO SYMBOLS AND ABBREVIATIONS:	
TOC	STRUCTURAL FLOOR LEVEL
TOC	TOP LEVEL OF STRUCTURAL CONCRETE
TOS	TOP LEVEL OF STEEL BEAM/COLUMN
FFL	FINISHED FLOOR LEVEL
RC	REINFORCED CONCRETE
PC	PRE-CAST
BM	BEAM'S
COL	COLUMN'S
CONC.	CONCRETE
	GRID LINE / CENTRE LINE
IJ	ISOLATION JOINT
LJ	LONGITUDINAL JOINT
TJ	TRANSVERSE JOINT
MJ	MOVEMENT JOINT
T.L.	TOP LEVEL
THK	THICK
HDG	HOT DIPPED GALVANIZED

LEGEND:	
	DEMOLITION EXISTING BLOCK WALL 215mm
	DEMOLITION EXISTING STONE WALL 500-600mm
	ex 215mm SOLID 7.5N BLOCKWORK WALL
	ex stonework
	DETAILED SECTION 1-1 SHOW ON DRG. T4988-S002
	MEANS REFER TO DRAWING T4988-S003 FOR DETAIL ENLARGED DETAIL '1'

	CF	CF	TENDER ISSUE	28.04.26
REV	REV	BY	APPROD	DESCRIPTION
				DATE

JA Gorman
consulting engineers
project managers

Forest Park,
Mullingar, Co. Westmeath.
Tel: 044-9347338 / 9347341
Fax: 044-9347400
Email: info@jagorman.ie
Web: www.jagorman.ie

CLIENT: CARROLLS IRISH GIFTS

PROJECT TITLE: IMMERSIVE EXPERIENCE TALBOT STREET DUBLIN

DRAWING TITLE: SECOND FLOOR PLAN DEMOLITION & TEMPORARY WORKS

PLOT SIZE: A1	PLOT SCALE: 1:50	DRAWN BY: CF	CHECKED BY: CF
APPROVED BY: JG	PROJECT No: 4988	DRAWING No: T4988-S005	REV: -

Copyright © J.A. Gorman Consulting Engineers Ltd. Unauthorised reproduction prohibited.