


Scope

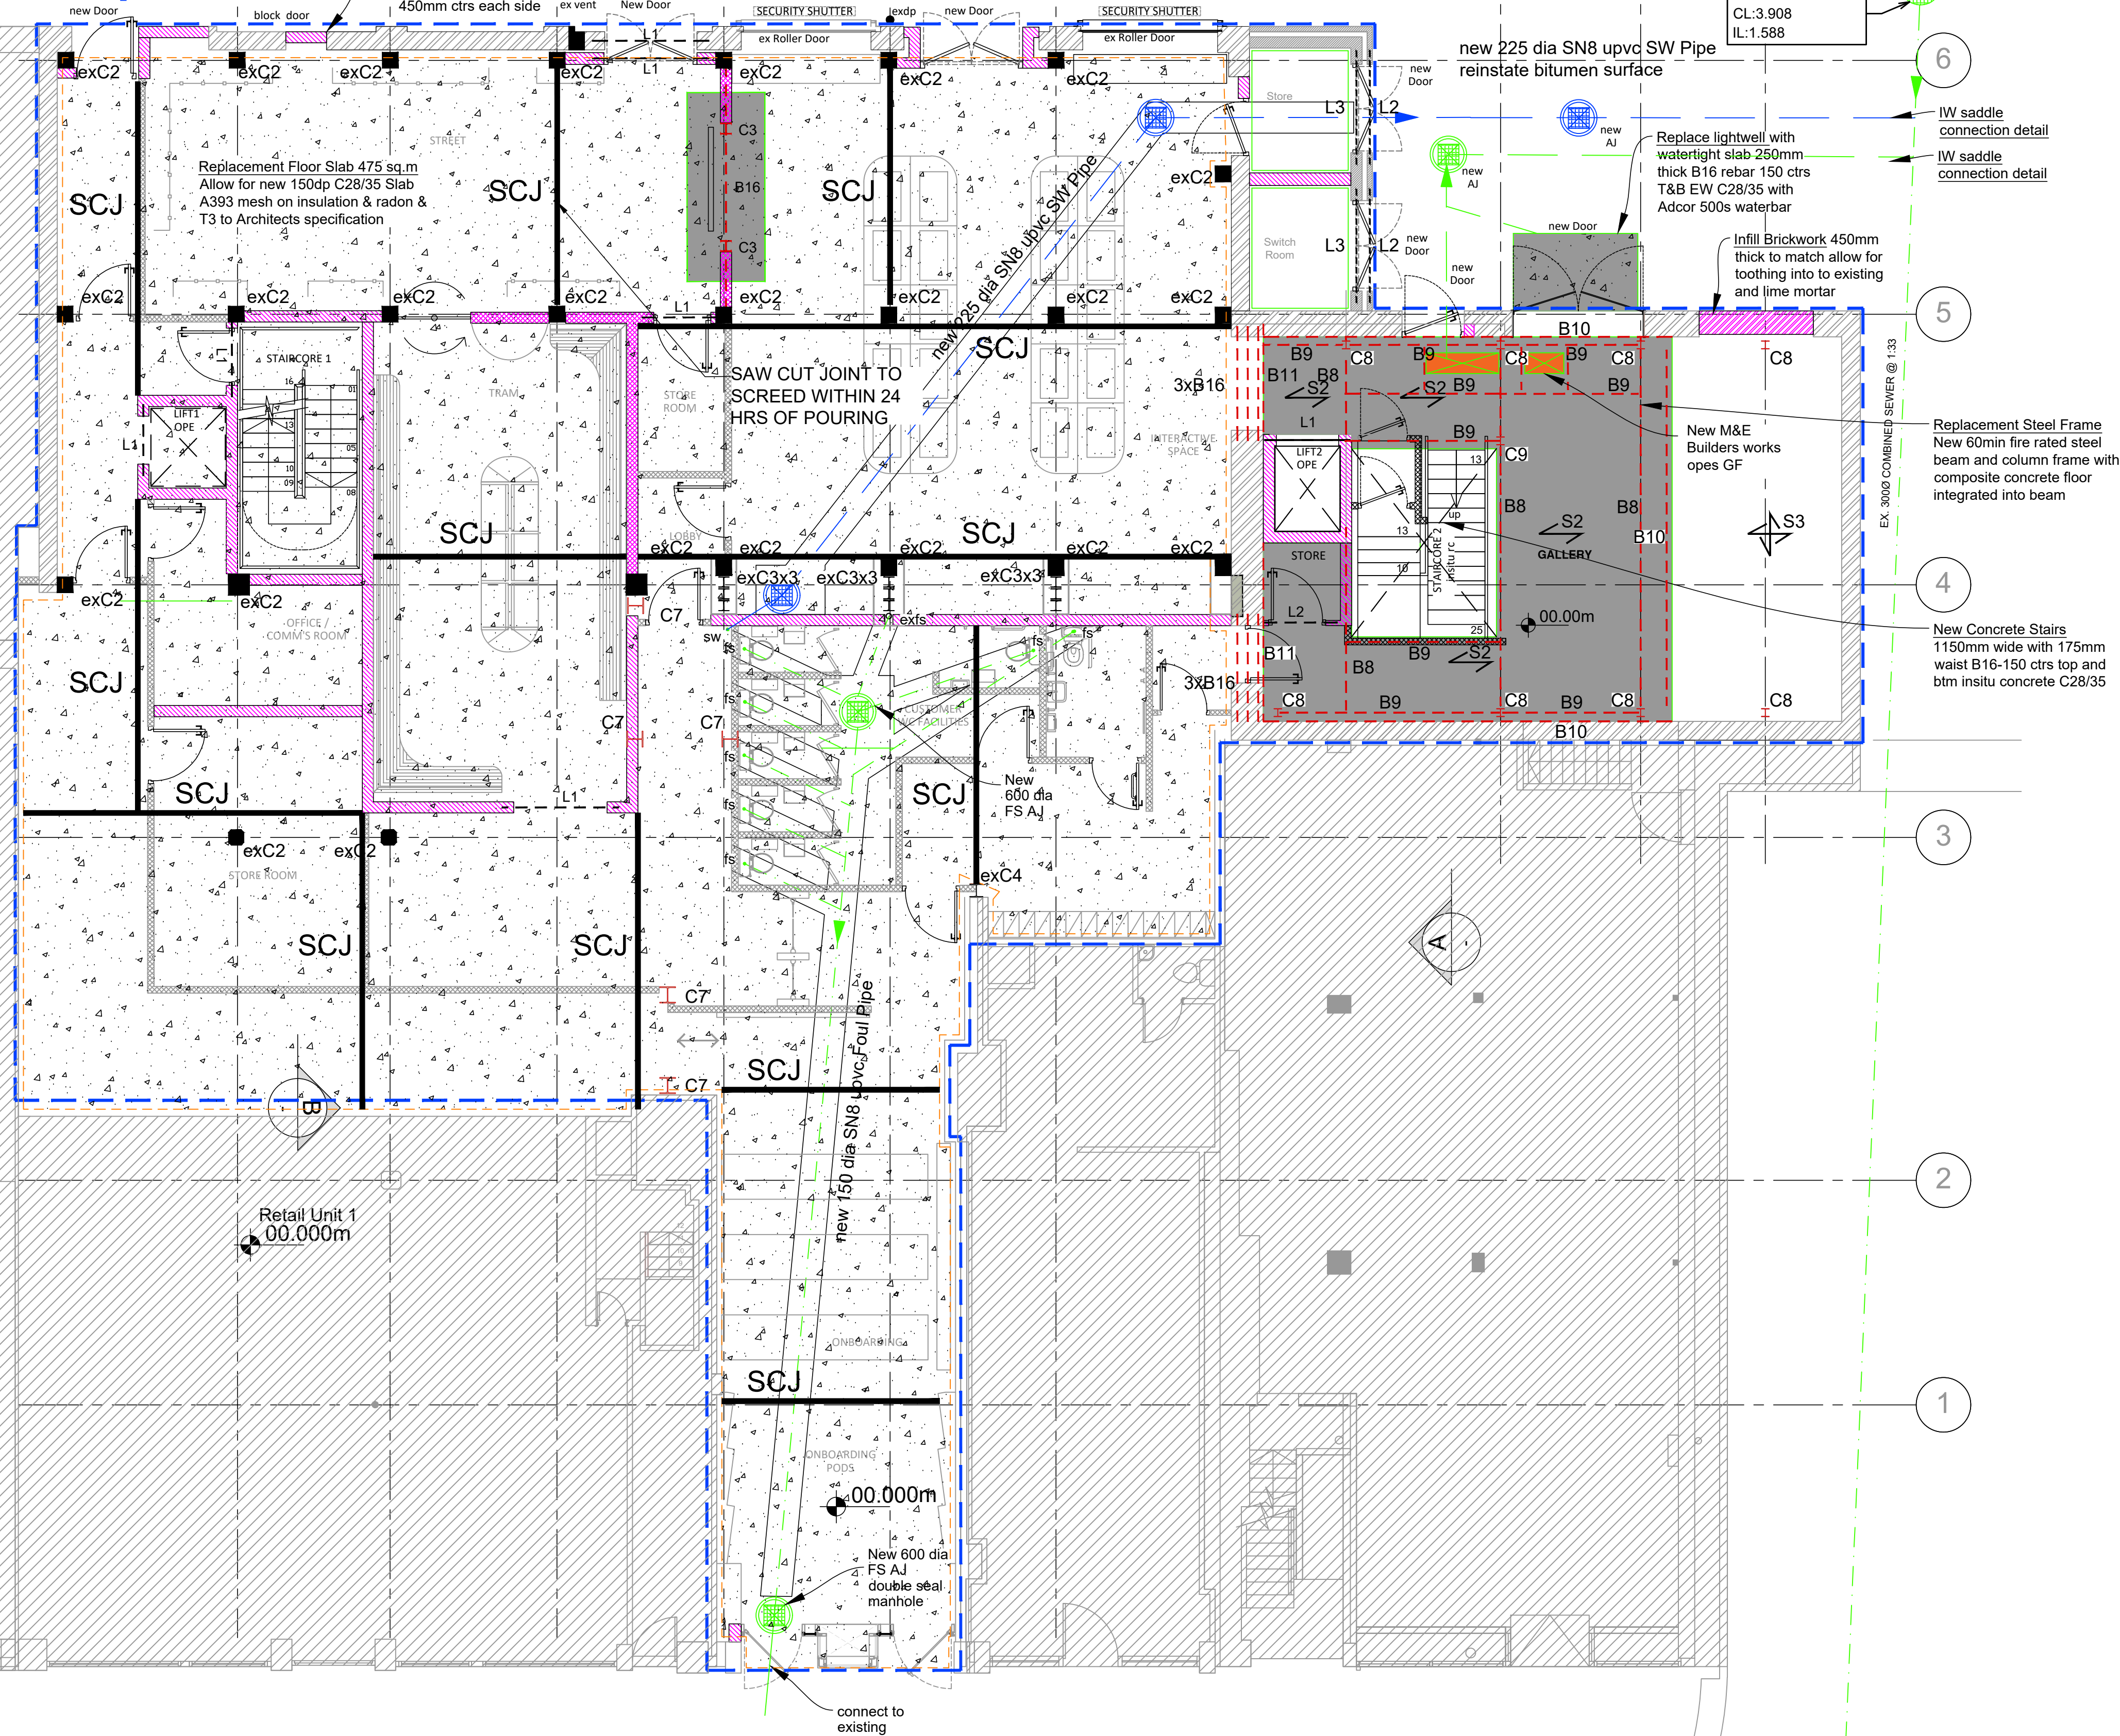

- GENERAL NOTES:
- DO NOT SCALE FROM THIS DRAWING
 - ALL DIMENSIONS ARE IN MM UNLESS NOTED OTHERWISE
 - THIS DRAWING IS TO BE READ IN CONJUNCTION WITH ALL RELEVANT ENGINEERS DRAWINGS, SPECIFICATIONS AND CONTRACT DOCUMENTS
 - ALL WORKS ARE TO BE IN ACCORDANCE WITH THE RELEVANT AND CURRENT HEALTH AND SAFETY LEGISLATION
 - SPECIFICATION OF THE WORKS TO BE TO THE APPROPRIATE EURO STANDARD OR THE EQUIVALENT BRITISH STANDARD
 - EXCAVATIONS FOR FOUNDATIONS TO BE INSPECTED BY THE ENGINEER PRIOR TO POURING OF THE FOUNDATIONS

- LEGEND:
- DEMOLITION EXISTING BLOCK WALL 215mm
 - DEMOLITION EXISTING STONE WALL 500-600mm
 - NEW SOLID 7.5N BLOCKWORK WALL
 - NEW STONE FACING REFER TO ARCH
 - L1 215x 65dp PRESTRESSED LINTEL 225mm BEARING
 - L2 100x 65dp PRESTRESSED LINTEL 225mm BEARING
 - L3 215x 215dp STONE LINTEL 225mm BEARING
 - GA1 120x120x12 RSA ANGLE HOT DIP GALV 450mm BEARING
 - RIISING CONCRETE OUTLINES
 - SPLAY/EDGE UNDER FLOOR SLAB
 - VOID IN CONCRETE
 - 1 S002 DETAILED SECTION 1-1 SHOW ON DRG. T4988-S002
 - 1 S003 MEANS REFER TO DRAWING T4988-S003 FOR DETAIL ENLARGED DETAIL '1'
 - DIRECTION OF SPAN OF SLAB

- MEMBER LEGEND
- STEEL S275 JO UNO
- C1 203x133ub
 - C2 152x127RSJ37 with 350x350 rc surround
 - C3 203uc46
 - C4 254uc73
 - C5 350x700 RC column
 - C6 350x1150 RC column
 - C7 305uc97
 - C8 152uc37 (S355)
 - C9 152uc44 (S355)
- B1 533x210ub122
- B2 203x102ub
- B3 203uc52
- B4 305uc97
- B5 305uc118
- B6 152x127RSJ37 with 350x350 rc surround
- B7 203x152RSJ52 300x600dp rc
- B8 178x102ub19 with 12mm x200 BTM Plate stitch welded
- B9 178x102ub19
- B10 200x90pfc
- B11 230x90pfc30
- B12 203uc60
- B13 305uc118
- B14 305x165ub60
- B15 254uc73
- B16 203uc46
- SLABS C28/35 (20mm)
- S1 450mm dp B20 150 EW T&B
 - S2 190dp Comflor 60 with A393
 - S3 450mm dp B20 150 EW T&B
 - S4 200-275 Comflor 60 with A393
 - S5 18mm OSB on 225x44 c16 JOISTS

REV	BY	DATE	DESCRIPTION
1	CF	28.04.26	TENDER ISSUE

TENDER ISSUE

JA Gorman
consulting engineers
project managers

Forest Park,
Mullingar, Co. Westmeath.
Tel: 044-9347338 / 9347341
Fax: 044-9347400
Email: info@jagorman.ie
Web: www.jagorman.ie

CLIENT: CARROLLS IRISH GIFTS

PROJECT TITLE: IMMERSIVE EXPERIENCE TALBOT STREET DUBLIN

DRAWING TITLE: PROPOSED GROUND FLOOR PLAN STRUCTURE

PLOT SIZE: A1	PLOT SCALE: As Shown	DRAWN BY: CF	CHECKED BY: CF
APPROVED BY: JG	PROJECT No: 4988	DRAWING No: T4988-S007	REV: -