A1

Do not scale drawing, work to figured dimensions. All dimensions to be checked on site. Any errors or discrepancies to be reported to MILLIMETRE DESIGN. This drawing may not be edited or modified without permission. This drawing is to be read in colour and in conjunction with all relevant consultant and specialist drawings, schedules and documentation. Only build from drawings issued as Construction.


Legend

- AREA OUTSIDE SCOPE OF WORKS
- LX.XX — INTERIOR ROOM No.
- DRX_XX — INTERIOR DOOR No.
- JTX_XX — FIXED JOINERY No.
- GSX_XX — INTERNAL GLAZED SCREEN No.
- GLX_XX — EXTERNAL GLAZING No.
- DLX_XX — EXTERNAL DOOR No.
- SPX_XX — SET PIECE No.
- 60min FIRE RESISTANCE BLOCKWORK
- 60min FIRE RESISTANCE PARTITION
- 30min FIRE RESISTANCE PARTITION
- NON FIRE RESISTANCE PARTITION
- INSULATED PLASTERBOARD
- 60min / ACOUSTIC INFILL PLASTERBOARD SECTIONS
- 60min SHAFTWALL PLASTERBOARD SECTIONS
- 60min FIRE RESISTANCE ACOUSTIC PARTITION
- 30min FIRE RESISTANCE ACOUSTIC PARTITION
- NFR ACOUSTIC PARTITION

Notes:

To be read in conjunction with all relevant drawings & schedules, refer to drawing register for breakdown of drawings.

Drawing to be printed in colour.

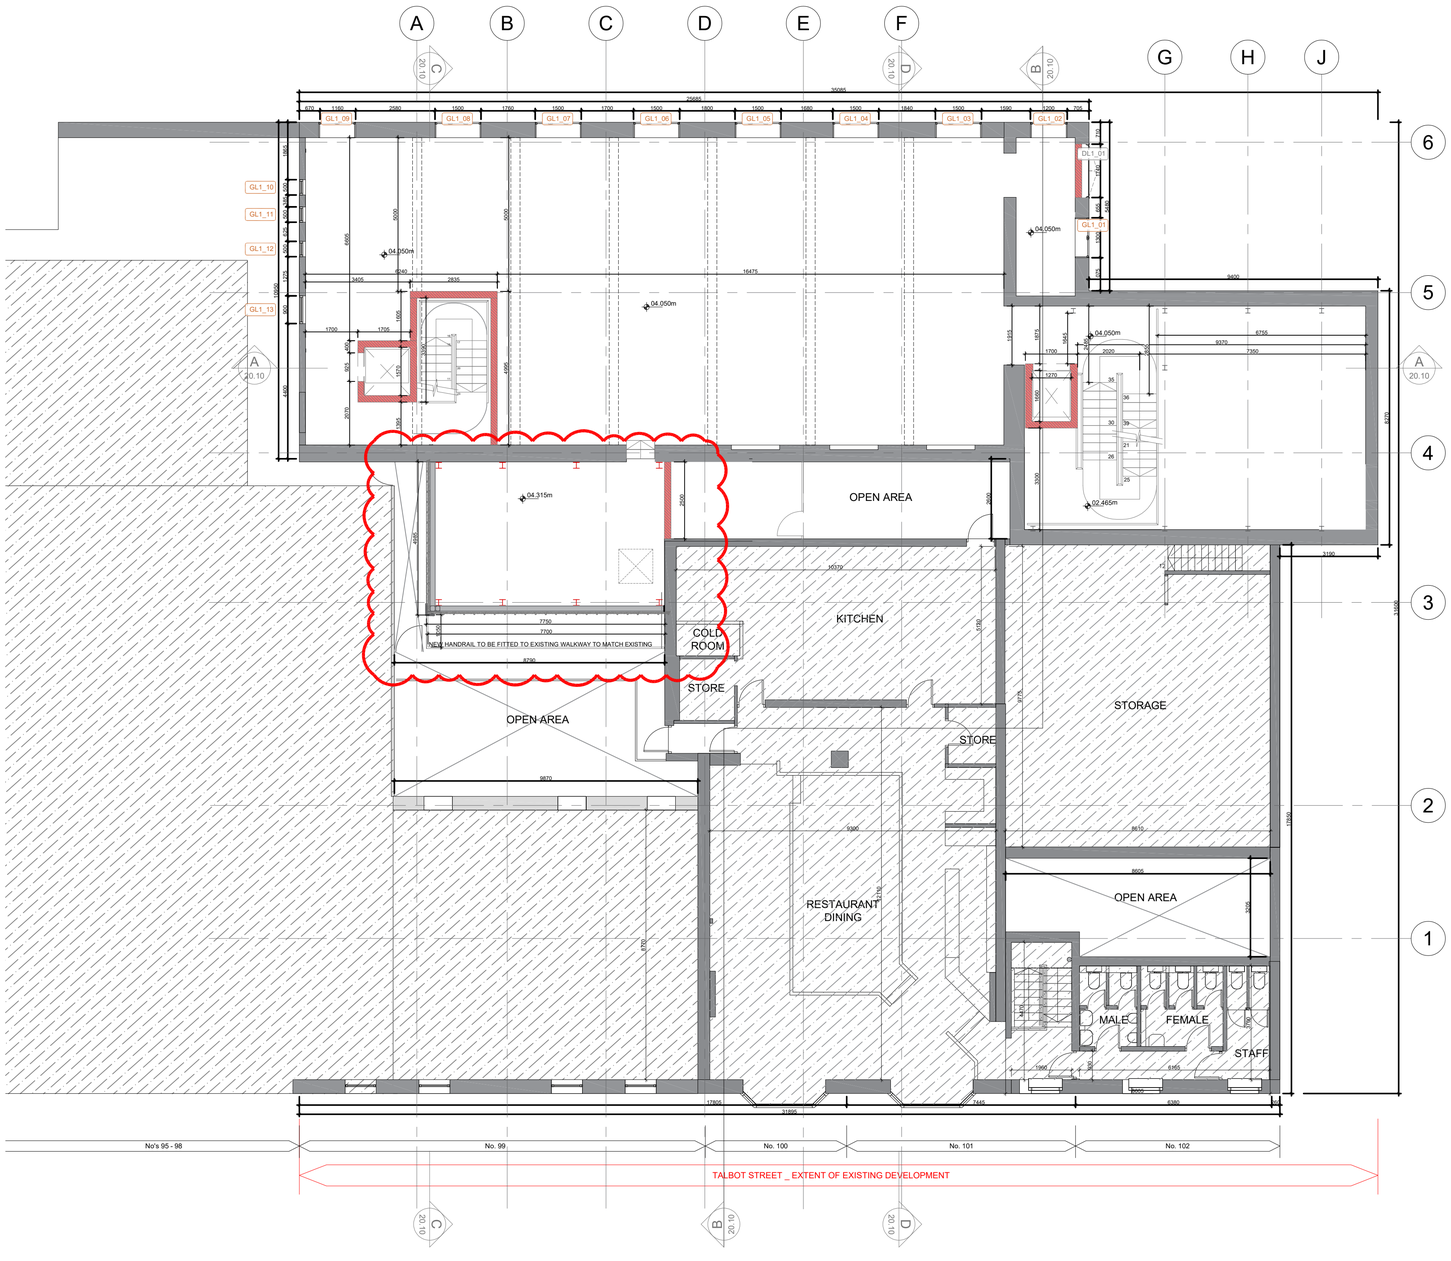

REV	DATE	APP BY	DESCRIPTION
C	29.04.26	SMC	UPDATED AS HIGHLIGHTED
B	13.03.26	SMC	ISSUED FOR TENDER
A	17.02.26	SMC	REVISED AS HIGHLIGHTED
#	26.01.26	SMC	FIRST ISSUE

MILLIMETRE DESIGN
4 Ongar Square, Ongar Village, Dublin 15. D15 H34C
+353 1 826 3971
info@millimetredesign.com
www.millimetredesign.com

This drawing is the property of Millimetre Design Ltd & must not be reproduced without prior consent.

CLIENT	Carrolls Irish Gifts Immersive Experience
PROJECT ADDRESS	Talbot Street, North City, Dublin 1, D01 X652
DWG TITLE	FIRST FLOOR PLAN PROPOSED WORKS
EDITION	TENDER
DWG NO	CIX-TD-11-11
REV	C
PROJECT NO	CIX
SCALE	1:100
DATE	MAR 2026
DRN	SMC
APP	

MILLIMETRE DESIGN issues this drawing (and associated Schedules) with the following conditions and understandings: Upon receipt of same, we understand that the recipient accepts these terms and conditions: The information contained herein, where issued for Planning / Tender , must not be used for the coordination and/or construction of this project. Only build from drawings issued as 'Construction'. MILLIMETRE DESIGN does not take responsibility for information scaled off drawings, any measurements taken from information that is not dimensioned, is at the risk of the recipient All dimensions must be checked on site. Any discrepancies herein or within associated documents, to be reported to MILLIMETRE DESIGN immediately. The recipient is responsible for checking that the information as issued herein is correct and complete, by consulting with all other information as issued as part of this package and during the course of the project, inclusive of checking all dimensions on site. This drawing may not be edited or modified without permission from MILLIMETRE DESIGN. This drawing is to be read in colour and in conjunction with all relevant consultant and specialist drawings, schedules and documentation (both hard copy and /or soft copy information issued). MILLIMETRE DESIGN accepts no liability or responsibility for any loss or damage suffered by the recipient, arising out of, or in connection with, the use or misuse of the information issued or contained herein or within the associated schedules as issued as part of this pack. The original documents and their copyright, remain the property of MILLIMETRE DESIGN . The information contained herein is for the intended recipient only. In the event that the information contained herein is changed in any way, all references to MILLIMETRE DESIGN must be removed, and the total responsibility thereon of said changes, become that of the person / company / contractor making those changes. Revised drawings and documents may be issued electronically (soft copy) and /or manually (hard copy) and it is the responsibility of the recipient to ensure that they are working to current drawings/documents, at all times. In the event that the information contained herein is altered or added to in any way, all references to MILLIMETRE DESIGN must be removed and the total responsibility thereon of said alterations / additions, become that of the person/company/contractor making those changes or additions. Compliance with all Building Regulations, Fire Safety Certificate Approvals, Disabled Access Certificate approvals, and Planning Permission approvals, is the responsibility of the Building Contractor. All information is issued on the express understanding that the recipient accepts these limitations and disclaimers. The terms "document" and "information" in the above, refers to both text documents and drawings in either "hard copy or electronic format"